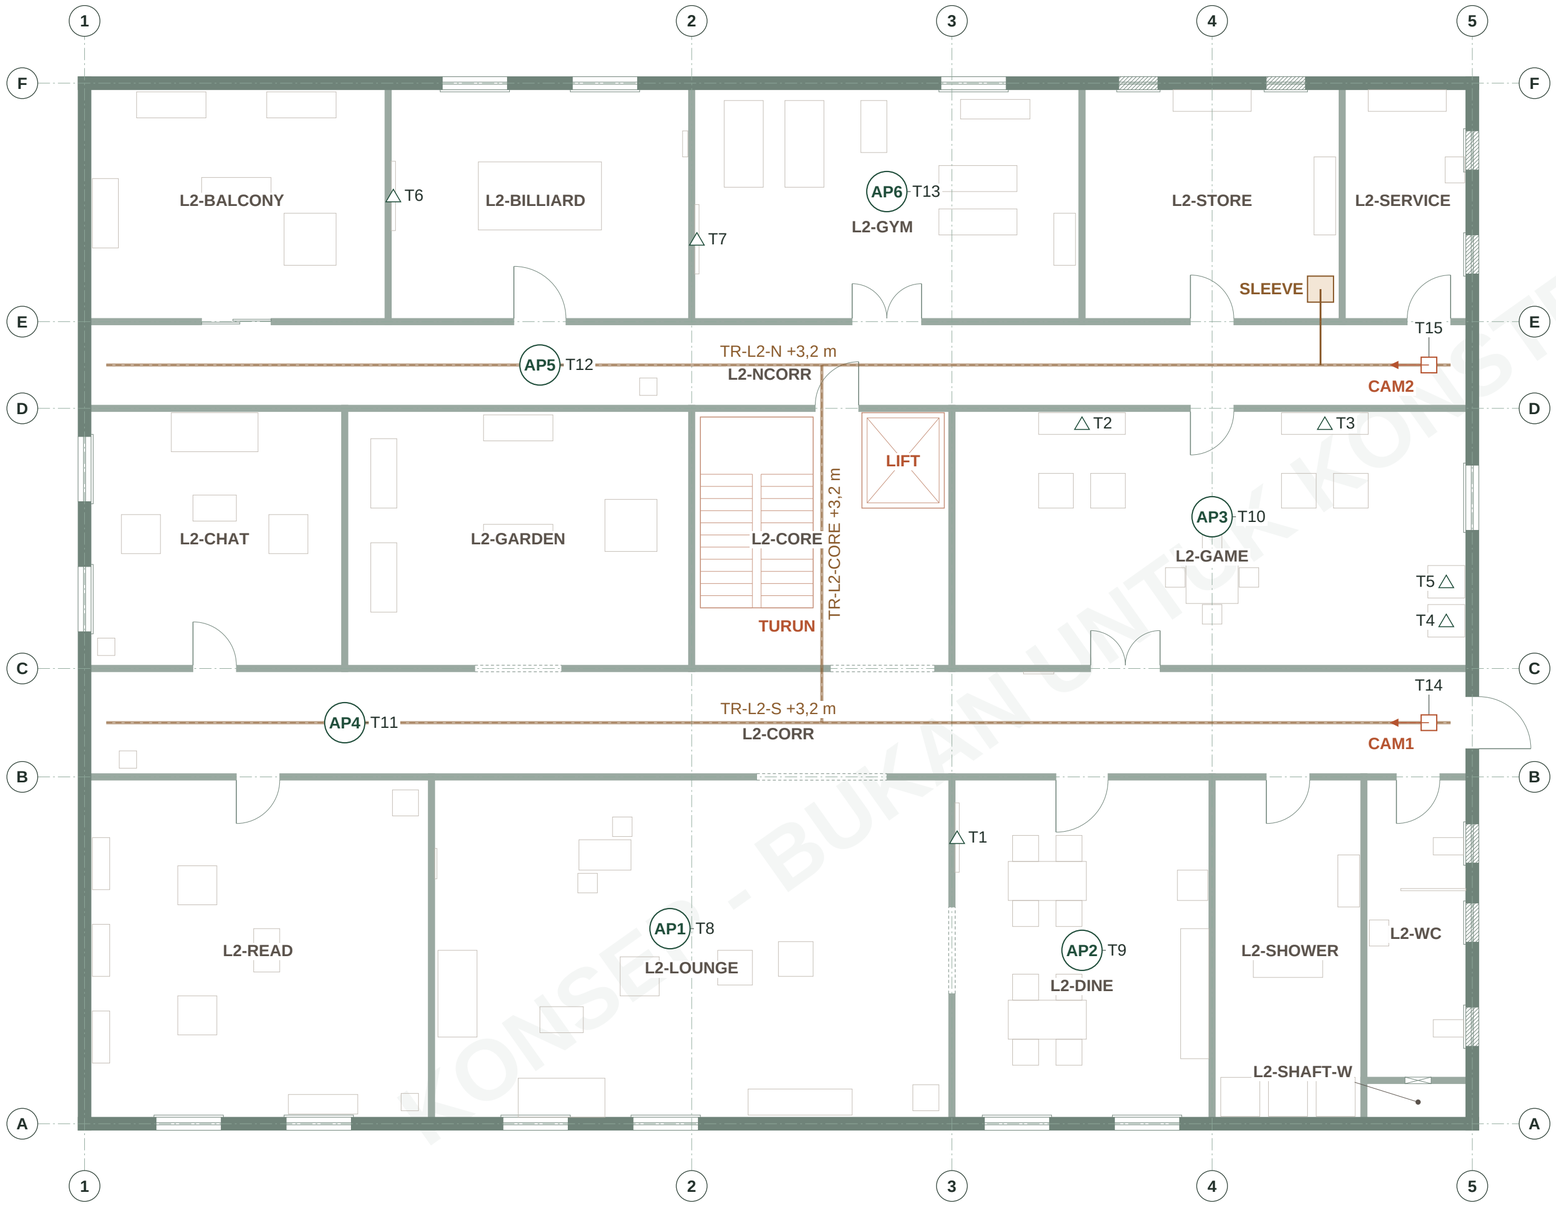

OUTLET, AP DAN KAMERA LANTAI 2 Skala 1:100 @ A2

Tag Tnn = outlet TO-L2-0nn, APn/CAMn = perangkat; ID lengkap di tabel panel. Tray di +3,2 m (AS-ICT-02). AP placeholder tanpa klaim radius Wi-Fi (AS-ICT-01).

0 1 2 5 10 m (1:100)

U

Rancangan virtual, bukan topologi produksi

Lantai L2: Lantai 2 - Rekreasi. Sumber: world.json ict + design/derived/ict-portmap.json

LEGENDA

- △ Outlet data, tag Tnn
- ○ AP placeholder, tag APn
- Kamera opsional + arah konsep
- Tray kabel +3,2 m
- Sleeve backbone ke lantai lain
- Rack 42U (target)

OUTLET L2 (15 outlet, 17 port)

Tag	ID	Ruang	Port
T1	TO-L2-001	DINE	1
T2	TO-L2-002	GAME	2
T3	TO-L2-003	GAME	2
T4	TO-L2-004	GAME	1
T5	TO-L2-005	GAME	1
T6	TO-L2-006	BILLIARD	1
T7	TO-L2-007	GYM	1
T8	TO-L2-008	LOUNGE	1

Tag	ID	Ruang	Port
T9	TO-L2-009	DINE	1
T10	TO-L2-010	GAME	1
T11	TO-L2-011	CORR	1
T12	TO-L2-012	NCORR	1
T13	TO-L2-013	GYM	1
T14	TO-L2-014	CORR	1
T15	TO-L2-015	NCORR	1

Domain dan endpoint per port: ICT-401.

PERANGKAT L2 (AP 6, kamera 2)

Tag	ID	Ruang	Outlet	z m	PoE
AP1	AP-L2-01	LOUNGE	T8	3,0	4
AP2	AP-L2-02	DINE	T9	3,0	4
AP3	AP-L2-03	GAME	T10	3,0	4
AP4	AP-L2-04	CORR	T11	3,0	4
AP5	AP-L2-05	NCORR	T12	3,0	4
AP6	AP-L2-06	GYM	T13	3,0	4
CAM1	CAM-L2-01	CORR	T14	2,8	3
CAM2	CAM-L2-02	NCORR	T15	2,8	3

Semua AP placeholder (AS-ICT-01); kamera opsional konsep, arah bukan FOV terukur. Lihat juga AS-ICT-02, AS-ICT-03, AS-NET-01 di A-001.

KONSEP - BUKAN UNTUK KONSTRUKSI

STATUS KONSEP Bukan untuk konstruksi

kantor-rpg Proyek kantor-rpg · gedung KRPG-01

Outlet, AP dan kamera Lantai 2

Skala 1:100 @ A2 lanskap
Revisi P03 · 2026-10-01
Render 2026-10-13 01:12:51 UTC
Halaman 1/1
Digambar Claude Code cloud (generator)
Diperiksa Max (supervisor) belum review
Sumber world.json sha256 38f94d70975b0c42

Nomor lembar **ICT-102** Rev P03 · 1/1

Huruf: Helvetica fallback (Alegreya Sans tidak tersedia saat build).