kantor-rpg

Paket gambar konsep · revisi P03 (2026-10-01)

KONSEP - bukan untuk konstruksi. Semua ukuran proposal untuk review.

INDEKS LEMBAR (dari design/sheets.json)

ID	Judul	Disiplin	Ukuran	Skala	Rev	Hlm	Status
A-001	Cover, indeks dan catatan umum	A	A3	NTS	P03	1	produced (konsep)
A-101	Denah Lantai 1	A	A2	1:100	P03	1	produced (konsep)
A-102	Denah Lantai 2	A	A2	1:100	P03	1	produced (konsep)
A-103	Room schedule, pintu dan jendela	A	A3	NTS	P03	2	produced (konsep)
A-201	Layout furniture Lantai 1	A	A2	1:100	P03	2	produced (konsep)
A-202	Layout furniture Lantai 2	A	A2	1:100	P03	2	produced (konsep)
A-301	Tampak	A	A3	1:200	P03	1	produced (konsep)
A-401	Potongan	A	A3	1:100	P03	1	produced (konsep)
I-101	Finish interior dan material	I	A3	1:200	P03	1	produced (konsep)
ICT-001	Topologi jaringan (virtual)	ICT	A3	NTS	P03	1	produced (konsep)
ICT-101	Outlet, AP dan kamera Lantai 1	ICT	A2	1:100	P03	1	produced (konsep)
ICT-102	Outlet, AP dan kamera Lantai 2	ICT	A2	1:100	P03	1	produced (konsep)
ICT-201	Elevasi rack	ICT	A3	1:10	P03	1	produced (konsep)
ICT-301	Pathway dan backbone	ICT	A3	1:200	P03	1	produced (konsep)
ICT-401	Port dan device schedule	ICT	A3	NTS	P03	3	produced (konsep)

Total 15 lembar, 20 halaman PDF (berkas gabungan drawings/pdf/kantor-rpg-sheets-all.pdf, label halaman = ID lembar).

LEGENDA STATUS

produced (konsep)	DXF + PDF dihasilkan generator dari world.json dan dibuka ulang oleh test.
target	Belum diproduksi.
DWG native	BLOCKED: AutoCAD berlisensi tidak tersedia di container cloud. DXF bukan DWG; lihat cad/AUTOCAD-RUNBOOK.md.

CATATAN UMUM

- Satuan: dimensi gambar dalam mm (DXF model space 1:1 mm, $INSUNITS = 4), luas dalam m², elevasi dalam m. Origin (0,0) sudut barat daya L1; X timur, Y utara.
- Semua lembar adalah KONSEP untuk review, bukan gambar konstruksi bertanda tangan. Ukuran adalah proposal (AS-DIM-01), bukan lahan, struktur, atau okupansi yang disahkan (AS-SITE-01).
- ICT adalah rancangan virtual, bukan topologi atau perangkat produksi (AS-NET-01).

DAFTAR ASUMSI (20, dari world.json)

AS-DIM-01	Footprint 32 m x 24 m per lantai dan tinggi antar lantai 4,0 m adalah proposal PRD, bukan luas lahan yang disahkan.
AS-DIM-02	Polygon ruang diukur pada garis as dinding; luas adalah luas as-drawn, bukan luas bersih/usable.
AS-DIM-03	Tebal dinding konsep: luar 0,30 m, dalam 0,15 m; plafon 3,0 m; slab 0,30 m. Belum ada desain struktur.
AS-DIM-04	Ukuran furniture dari catalog adalah target konsep (bukan katalog vendor). Meja biliar 9 ft memakai luas main 2,54 x 1,27 m dan clearance stik 1,47 m sebagai target ukuran umum, wajib dicek ulang ke spesifikasi produk.
AS-DIM-05	Tangga U: 24 riser x 0,1667 m, tread 0,28 m, lebar flight 1,2 m. Target konsep game; tidak menyatakan tangga layak konstruksi.
AS-OCC-01	Faktor beban hunian memakai IBC 2021 Table 1004.5 sebagai pembanding, bukan regulasi Indonesia yang berlaku. Perhitungan egress resmi butuh profesional.
AS-OCC-02	Kapasitas kursi dihitung dari fixture; bukan target okupansi manusia yang diputuskan Budi.
AS-EXIT-01	Tangga darurat timur L2 hanya penanda konsep di luar envelope; jalur keluar belum dinilai memenuhi peraturan.
AS-ICT-01	Jumlah AP adalah placeholder; belum ada model site/material dan target coverage. Tidak ada radius Wi-Fi efektif yang diklaim.
AS-ICT-02	Slack kabel: 3,0 m sisi rack + 0,3 m sisi outlet; tray pada 3,2 m di atas lantai jadi; outlet meja 0,3 m; outlet plafon 3,0 m. Asumsi proyek, bukan standar.
AS-ICT-03	Batas panjang permanent link 90 m dipakai sebagai target konsep (praktik umum kabel tembaga terstruktur), wajib diverifikasi ke standar yang dipilih.
AS-ICT-04	Daya PoE worst-case per kelas memakai nilai PSE IEEE 802.3af/at/bt (Class 3 = 15,4 W, Class 4 = 30 W). Kelas perangkat placeholder sampai datasheet dipilih.
AS-ICT-05	Harga dan pengadaan belum ditentukan; tidak ada harga dalam paket ini. Rating UPS dan panas ICT memakai model referensi konsep (AS-ICT-07/08); sizing AC/listrik oleh MEP.
AS-ICT-06	Clearance rack depan 1,2 m / belakang 0,9 m adalah target konsep; verifikasi ke standar/panduan yang dipilih.
AS-ICT-07	Model referensi (USW-Pro-48-POE, USW-Pro-Aggregation, UDM-Pro-Max, R760xs PSU 600 W, RS2423+, OL3000ERTXL2U) dipilih untuk menutup gate PoE/UPS/panas konsep dari datasheet vendor bertanggal 2026-10-04. Bukan keputusan pengadaan; revisi hardware dan konfigurasi final wajib dicek ulang.
AS-ICT-08	Metode daya: switch dengan PD memakai plafon vendor termasuk PoE, tanpa switch memakai maksimum vendor tanpa PoE; server = rating PSU aktif / efisiensi 0,90 (asumsi); PF beban 0,90 (asumsi); margin 1,25; allowance aksesori 30 W (asumsi). Panas ruang server = input AC dikurangi daya PD yang keluar ruang + disipasi UPS vendor; rugi kabel PoE dihitung di ruang server (konservatif). Runtime UPS dan sizing AC belum dievaluasi.
AS-ICT-09	Target otonomi UPS 10 menit pada beban terhubung (Budi, 2026-10-05). Runtime dibaca dari kurva vendor (baterai baru) dengan interpolasi linier, lalu dikali 0,8 untuk penuaan baterai (asumsi). Baterai internal saja tidak cukup; 1 EBM BPE72V60ART2U ditambahkan sebagai model referensi, bukan keputusan pengadaan.
AS-NET-01	Domain jaringan office/demo/guest/lab/server adalah ID abstrak; bukan subnet, VLAN atau perangkat produksi.
AS-PERF-01	Target FPS/transfer/triangle adalah target PRD; angka hanya disebut terukur setelah benchmark tercatat.
AS-SITE-01	Lahan fisik, lokasi, budget, hosting dan okupansi manusia belum diputuskan.

KONSEP - BUKAN UNTUK KONSTRUKSI

STATUS KONSEP — Bukan untuk konstruksi

kantor-rpg Proyek kantor-rpg · gedung KRPG-01

Cover, indeks dan catatan umum


Skala	NTS @ A3 lanskap
Revisi	P03 · 2026-10-01
Render	2026-10-13 01:12:51 UTC
Halaman	1/1
Digambar	Claude Code cloud (generator)
Diperiksa	Max (supervisor) belum review
Sumber	world.json sha256 38f94d70975b0c42

Huruf: Helvetica fallback (Alegreya Sans tidak tersedia saat build).

Nomor lembar

A-001

Rev P03 · 1/1

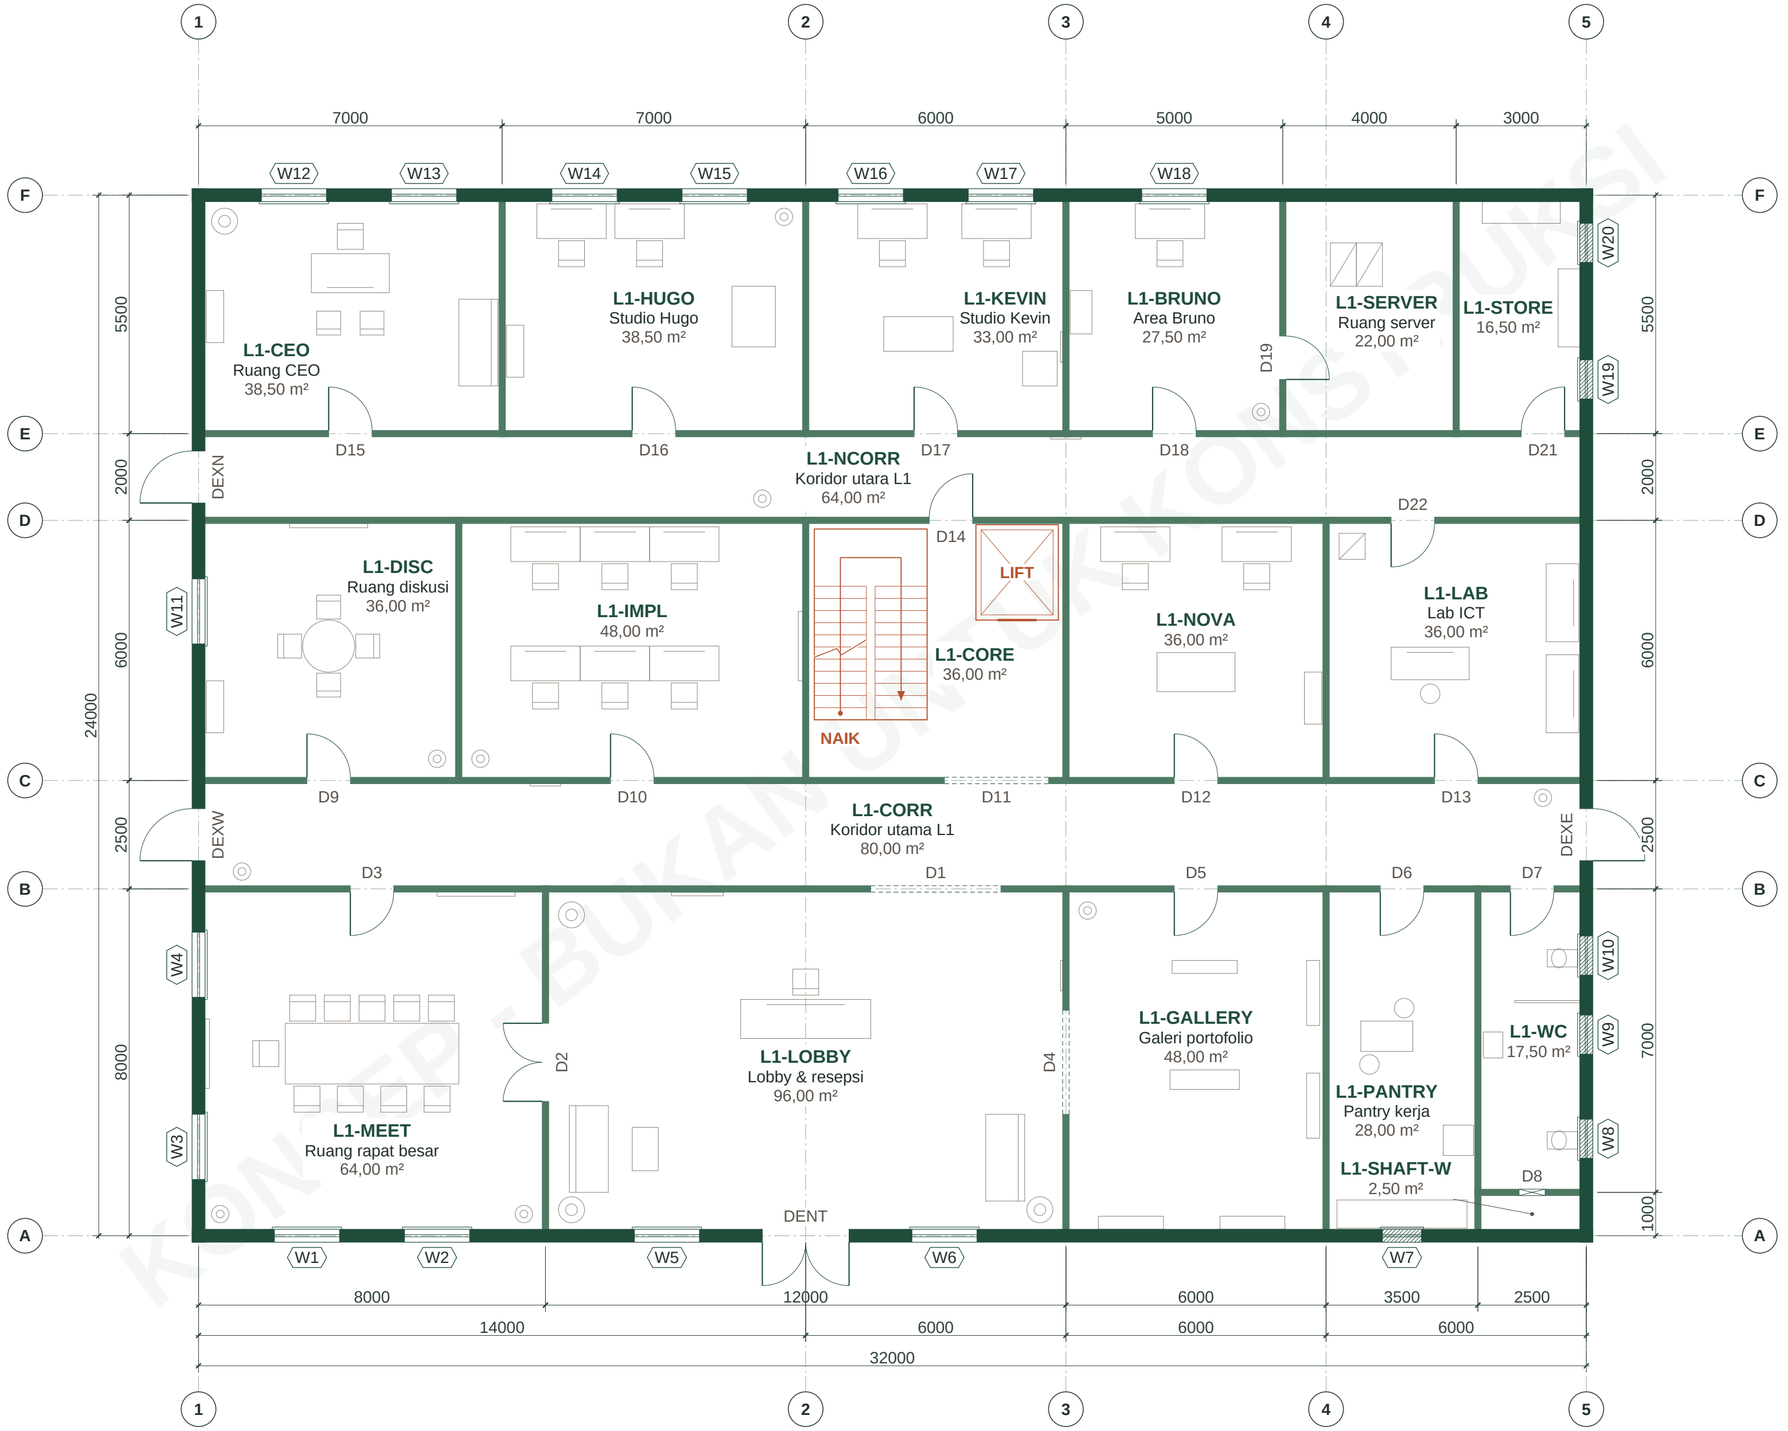

KONSEP · BUKAN UNTUK KONSTRUKSI

DENAH LANTAI 1

Skala 1:100 @ A2 · lantai L1
Ukuran dalam mm, as ke as dinding

0 1 2 5 10 m
Benar pada cetak A2 100%: 10 m = 100 mm

L2	+4,00 m	Rekreasi
L1	±0,00 m	**Kerja & Kunjungan (lembar ini)**

Utara = sumbu Y+ dunia
Origin (0,0) sudut barat daya L1, X timur. Grid acuan konsep (1..n, A..n), bukan grid struktur (AS-DIM-03).

LEGENDA

Dinding luar 0,30 m	Dinding dalam 0,15 m
Pintu tunggal, buka 90°	Pintu ganda
Bukaan tanpa daun	Akses shaft / riser
Furniture (AS-DIM-04)	Tangga U / lift
1 Grid acuan konsep	8000 Dimensi mm, as ke as
ID Tag ruang: ID, nama, luas	Dnn Tag pintu Dnn
Jendela bening, tag Wnn	Jendela kaca buram

DAFTAR RUANG L1 (luas as-drawn)

ID	Nama	Luas
L1-MEET	Ruang rapat besar	64,00 m²
L1-LOBBY	Lobby & resepsi	96,00 m²
L1-GALLERY	Galeri portofolio	48,00 m²
L1-PANTRY	Pantry kerja	28,00 m²
L1-SHAFT-W	Shaft basah	2,50 m²
L1-WC	Toilet aksesibel	17,50 m²
L1-CORR	Koridor utama L1	80,00 m²
L1-DISC	Ruang diskusi	36,00 m²
L1-IMPL	Ruang implementasi & review	48,00 m²
L1-CORE	Inti tangga & lift L1	36,00 m²
L1-NOVA	Area Nova (spesifikasi ICT)	36,00 m²
L1-LAB	Lab ICT	36,00 m²
L1-NCORR	Koridor utara L1	64,00 m²
L1-CEO	Ruang CEO	38,50 m²
L1-HUGO	Studio Hugo	38,50 m²
L1-KEVIN	Studio Kevin	33,00 m²
L1-BRUNO	Area Bruno	27,50 m²
L1-SERVER	Ruang server	22,00 m²
L1-STORE	Gudang & utilitas	16,50 m²
Jumlah 19 ruang		**768,00 m²**

= envelope 32 x 24 m (768,00 m²)

CATATAN

- Sumber tunggal design/world.json revisi P03; dinding dari tools/kantor/geometry.py.
- Pintu: arah buka dan engsel dari doors[].swing. Tag Dnn = pintu D-L1-nn; daftar di A-103.
- Jendela: 20 di lantai ini, 6 buram. Tag Wnn = W-L1-0nn; ambang dan kepala di A-103 dan A-301.
- Lantai L1: 19 ruang, 25 pintu/bukaan, 110 fixture, 42 slot duduk (AS-OCC-02). Exit konsep: 4, belum dinilai terhadap peraturan (AS-OCC-01).
- Asumsi AS-DIM-01, AS-DIM-02, AS-DIM-04 dan AS-DIM-05: teks lengkap di A-001.
- DXF pasangan cad/out/A-101.dxf (mm, 1:1). DWG native BLOCKED, lihat cad/AUTOCAD-RUNBOOK.md.

RIWAYAT REVISI

Rev	Tanggal	Keterangan
P03	2026-10-01	Hardening: arah bukaan pintu dan jendela konsep di dataset; gym provisional (Q-03). Lembar dihasilkan dari world.json revisi ini.

kantor-rpg Proyek kantor-rpg · gedung KRPG-01

STATUS KONSEP Bukan untuk konstruksi


Denah Lantai 1

L1: Lantai 1 - Kerja & Kunjungan

Skala	1:100 @ A2 lanskap
Revisi	P03 · 2026-10-01
Render	2026-10-13 01:12:51 UTC
Satuan	mm (dimensi), m² (luas)
Digambar	Claude Code cloud (generator)
Diperiksa	Max (supervisor) belum review
Sumber	world.json sha256 38f94d70975b0c42
Generator	cad/generate.py v1

Nomor lembar
A-101
Rev P03

Huruf: Helvetica fallback (Alegreya Sans tidak tersedia saat build).

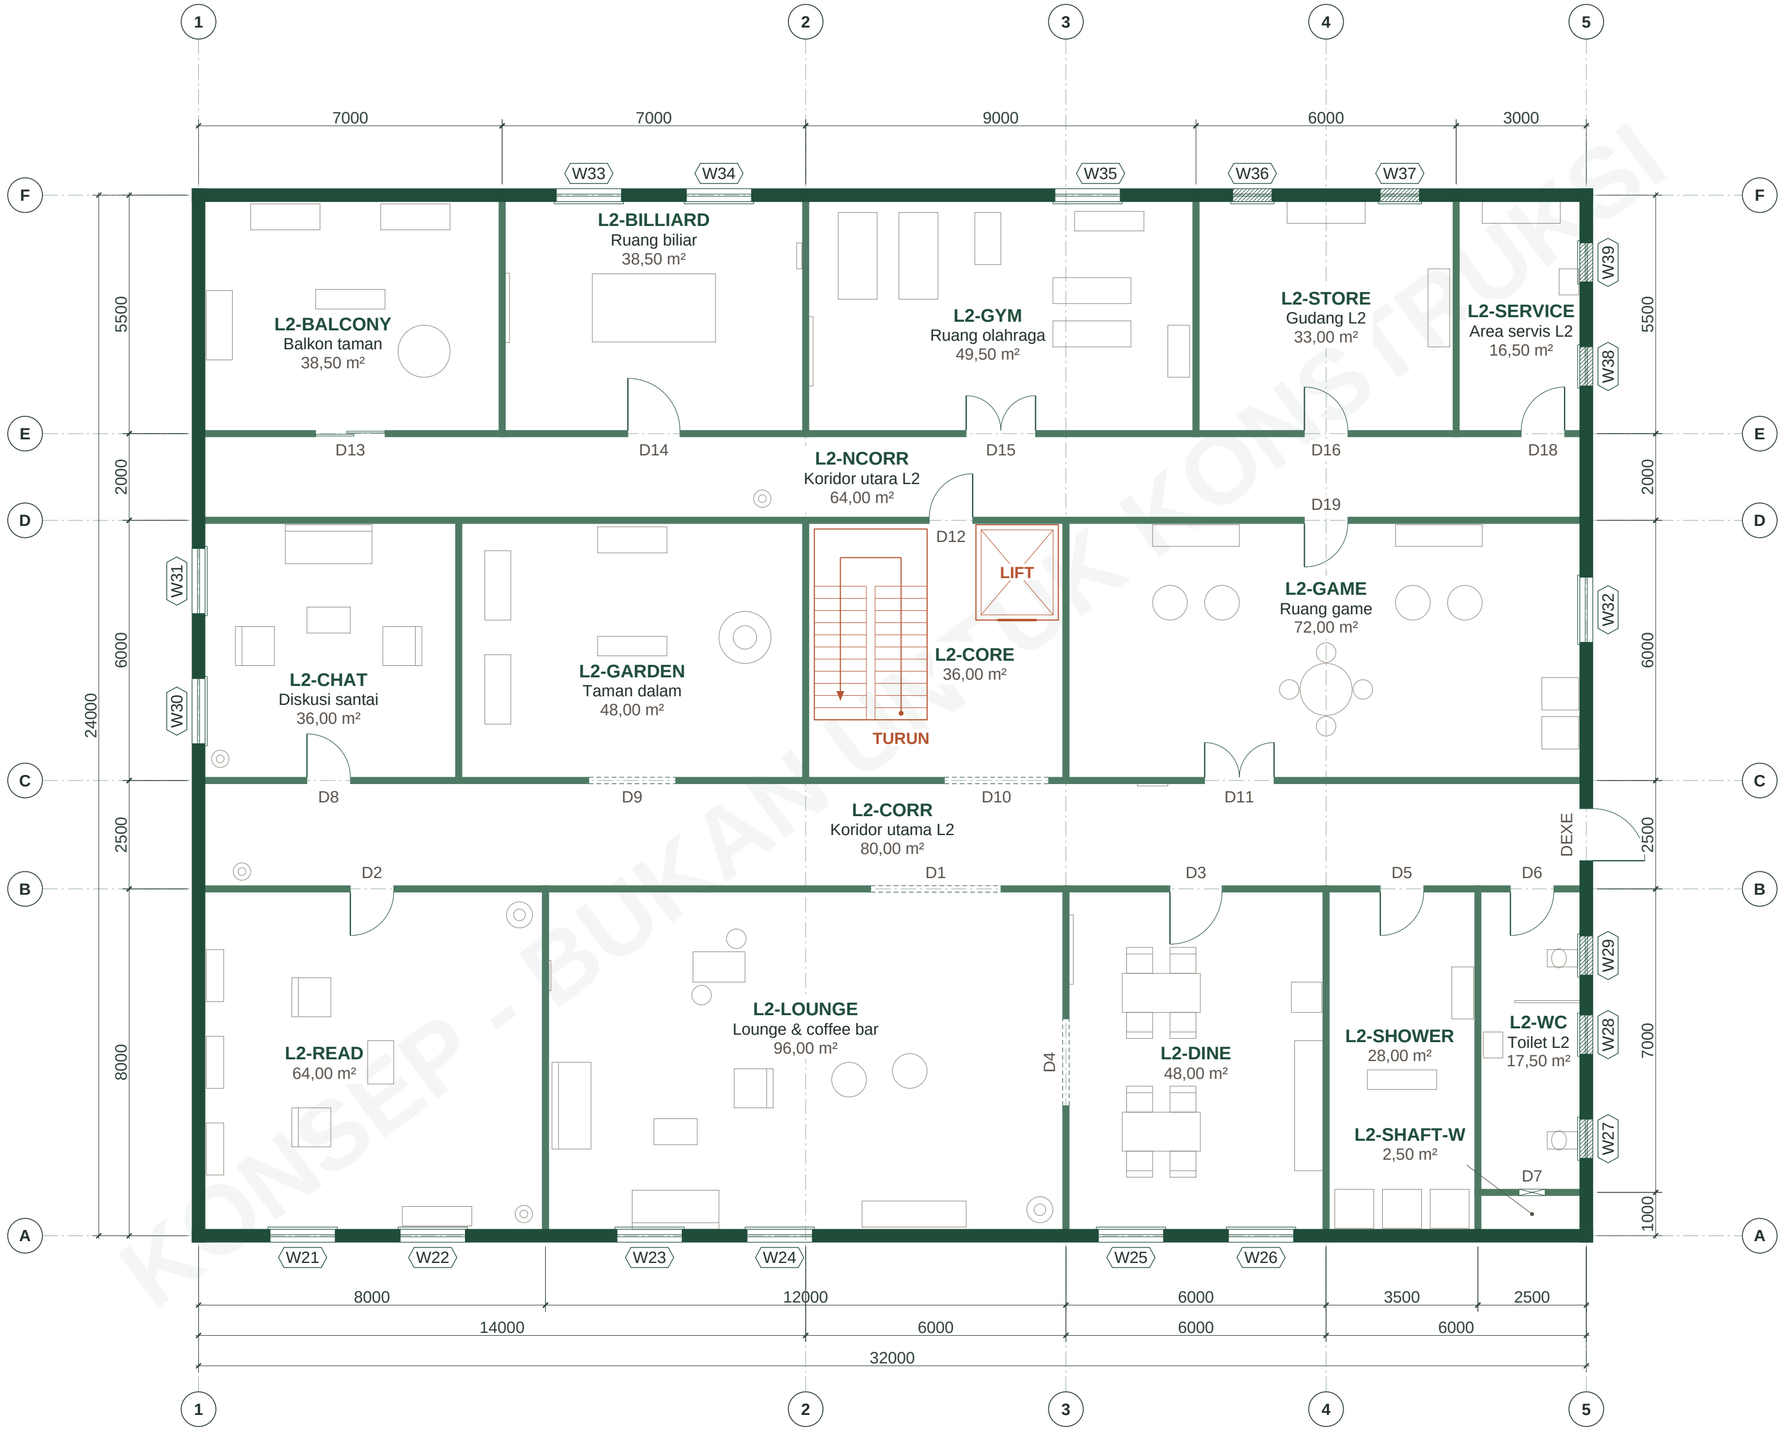

KONSEP - BUKAN UNTUK KONSTRUKSI

DENAH LANTAI 2

Skala 1:100 @ A2 · lantai L2
Ukuran dalam mm, as ke as dinding

0 1 2 5 10 m
Benar pada cetak A2 100%: 10 m = 100 mm

L2	+4,00 m	**Rekreasi (lembar ini)**
L1	±0,00 m	Kerja & Kunjungan

Utara = sumbu Y+ dunia
Origin (0,0) sudut barat daya L1, X timur. Grid acuan konsep (1..n, A..n), bukan grid struktur (AS-DIM-03).

LEGENDA

Dinding luar 0,30 m	Dinding dalam 0,15 m
Pintu tunggal, buka 90°	Pintu ganda
Bukaan tanpa daun	Akses shaft / riser
Furniture (AS-DIM-04)	Tangga U / lift
1 Grid acuan konsep	8000 Dimensi mm, as ke as
ID Tag ruang: ID, nama, luas	Dnn Tag pintu Dnn
Jendela bening, tag Wnn	Jendela kaca buram

DAFTAR RUANG L2 (luas as-drawn)

ID	Nama	Luas
L2-READ	Perpustakaan / reading nook	64,00 m²
L2-LOUNGE	Lounge & coffee bar	96,00 m²
L2-DINE	Ruang makan & pantry	48,00 m²
L2-SHOWER	Shower & ruang ganti	28,00 m²
L2-SHAFT-W	Shaft basah L2	2,50 m²
L2-WC	Toilet L2	17,50 m²
L2-CORR	Koridor utama L2	80,00 m²
L2-CHAT	Diskusi santai	36,00 m²
L2-GARDEN	Taman dalam	48,00 m²
L2-CORE	Inti tangga & lift L2	36,00 m²
L2-GAME	Ruang game	72,00 m²
L2-NCORR	Koridor utara L2	64,00 m²
L2-BALCONY	Balkon taman	38,50 m²
L2-BILLIARD	Ruang biliar	38,50 m²
L2-GYM	Ruang olahraga	49,50 m²
L2-STORE	Gudang L2	33,00 m²
L2-SERVICE	Area servis L2	16,50 m²
Jumlah 17 ruang		**768,00 m²**

= envelope 32 x 24 m (768,00 m²)

CATATAN

- Sumber tunggal design/world.json revisi P03; dinding dari tools/kantor/geometry.py.
- Pintu: arah buka dan engsel dari doors[].swing. Tag Dnn = pintu D-L2-nn; daftar di A-103.
- Jendela: 19 di lantai ini, 7 buram. Tag Wnn = W-L2-0nn; ambang dan kepala di A-103 dan A-301.
- Lantai L2: 17 ruang, 19 pintu/bukaan, 91 fixture, 42 slot duduk (AS-OCC-02). Exit konsep: 1, belum dinilai terhadap peraturan (AS-OCC-01).
- Asumsi AS-DIM-01, AS-DIM-02, AS-DIM-04 dan AS-DIM-05: teks lengkap di A-001.
- DXF pasangan cad/out/A-102.dxf (mm, 1:1). DWG native BLOCKED, lihat cad/AUTOCAD-RUNBOOK.md.
- VL-ESC-E: Tangga darurat luar (penanda konsep, perlu kajian); di luar envelope, tidak digambar (AS-EXIT-01).

RIWAYAT REVISI

Rev	Tanggal	Keterangan
P03	2026-10-01	Hardening: arah bukaan pintu dan jendela konsep di dataset; gym provisional (Q-03). Lembar dihasilkan dari world.json revisi ini.

kantor-rpg Proyek kantor-rpg · gedung KRPG-01

STATUS KONSEP Bukan untuk konstruksi

Denah Lantai 2

L2: Lantai 2 - Rekreasi

Skala	1:100 @ A2 lanskap
Revisi	P03 · 2026-10-01
Render	2026-10-13 01:12:51 UTC
Satuan	mm (dimensi), m² (luas)
Digambar	Claude Code cloud (generator)
Diperiksa	Max (supervisor) belum review
Sumber	world.json sha256 38f94d70975b0c42
Generator	cad/generate.py v1

Nomor lembar
A-102
Rev P03

Huruf: Helvetica fallback (Alegreya Sans tidak tersedia saat build).

ROOM SCHEDULE

NTS · luas as-drawn dari polygon (AS-DIM-02)

ID	Nama	Lantai	Kategori	Akses	Luas m²	Kursi	Pintu	Finish lantai	Finish dinding	Finish plafon
L1-MEET	Ruang rapat besar	L1	work	public	64,00	10	D-L1-02, D-L1-03	karpet tile matte	cat matte krem	akustik panel
L1-LOBBY	Lobby & resepsi	L1	public	public	96,00	5	D-L1-ENT, D-L1-01, D-L1-02, D-L1-04	vinyl motif kayu	cat matte krem + panel kayu	gypsum
L1-GALLERY	Galeri portofolio	L1	public	public	48,00	2	D-L1-04, D-L1-05	vinyl motif kayu	cat matte krem + panel kayu	gypsum
L1-PANTRY	Pantry kerja	L1	wet	staff	28,00	2	D-L1-06	keramik anti-slip	keramik dinding	gypsum tahan lembab
L1-SHAFT-W	Shaft basah	L1	shaft	restricted	2,50	0	D-L1-08	-	-	-
L1-WC	Toilet aksesibel	L1	wet	public	17,50	0	D-L1-07, D-L1-08	keramik anti-slip	keramik dinding	gypsum tahan lembab
L1-CORR	Koridor utama L1	L1	circulation	public	80,00	0	D-L1-01, D-L1-03, D-L1-05, D-L1-06, D-L1-07, D-L1-EXW, D-L1-EXE, D-L1-09, D-L1-10, D-L1-11, D-L1-12, D-L1-13	vinyl motif kayu	cat matte krem + panel kayu	gypsum
L1-DISC	Ruang diskusi	L1	quiet	staff	36,00	4	D-L1-09	karpet tile matte	cat matte krem	akustik panel
L1-IMPL	Ruang implementasi & review	L1	work	staff	48,00	6	D-L1-10	karpet tile matte	cat matte krem	akustik panel
L1-CORE	Inti tangga & lift L1	L1	circulation	public	36,00	0	D-L1-11, D-L1-14	vinyl motif kayu	cat matte krem + panel kayu	gypsum
L1-NOVA	Area Nova (spesifikasi ICT)	L1	work	staff	36,00	2	D-L1-12	karpet tile matte	cat matte krem	akustik panel
L1-LAB	Lab ICT	L1	work	staff	36,00	1	D-L1-13, D-L1-22	vinyl anti-statik (target)	cat matte	gypsum + akses tray
L1-NCORR	Koridor utara L1	L1	circulation	staff	64,00	0	D-L1-14, D-L1-22, D-L1-EXN, D-L1-15, D-L1-16, D-L1-17, D-L1-18, D-L1-21	vinyl motif kayu	cat matte krem + panel kayu	gypsum
L1-CEO	Ruang CEO	L1	quiet	staff	38,50	5	D-L1-15	karpet tile matte	cat matte krem	akustik panel
L1-HUGO	Studio Hugo	L1	work	staff	38,50	2	D-L1-16	vinyl motif kayu	cat matte krem + panel kayu	gypsum
L1-KEVIN	Studio Kevin	L1	work	staff	33,00	2	D-L1-17	vinyl motif kayu	cat matte krem + panel kayu	gypsum
L1-BRUNO	Area Bruno	L1	work	staff	27,50	1	D-L1-18, D-L1-19	vinyl anti-statik (target)	cat matte	gypsum + akses tray
L1-SERVER	Ruang server	L1	restricted	restricted	22,00	0	D-L1-19	vinyl anti-statik (target)	cat matte	gypsum + akses tray
L1-STORE	Gudang & utilitas	L1	service	staff	16,50	0	D-L1-21	epoxy	cat matte	gypsum
Subtotal L1	19 ruang				768,00	42	cek: jumlah = envelope 768,00 m² COCOK			
L2-READ	Perpustakaan / reading nook	L2	quiet	staff	64,00	4	D-L2-02	karpet tile matte	cat matte krem	akustik panel
L2-LOUNGE	Lounge & coffee bar	L2	recreation	staff	96,00	9	D-L2-01, D-L2-04	vinyl motif kayu	cat matte krem + panel kayu	gypsum
L2-DINE	Ruang makan & pantry	L2	recreation	staff	48,00	8	D-L2-03, D-L2-04	keramik anti-slip	keramik dinding	gypsum tahan lembab
L2-SHOWER	Shower & ruang ganti	L2	wet	staff	28,00	2	D-L2-05	keramik anti-slip	keramik dinding	gypsum tahan lembab
L2-SHAFT-W	Shaft basah L2	L2	shaft	restricted	2,50	0	D-L2-07	-	-	-
L2-WC	Toilet L2	L2	wet	staff	17,50	0	D-L2-06, D-L2-07	keramik anti-slip	keramik dinding	gypsum tahan lembab
L2-CORR	Koridor utama L2	L2	circulation	staff	80,00	0	D-L2-01, D-L2-02, D-L2-03, D-L2-05, D-L2-06, D-L2-EXE, D-L2-08, D-L2-09, D-L2-10, D-L2-11	vinyl motif kayu	cat matte krem + panel kayu	gypsum
L2-CHAT	Diskusi santai	L2	quiet	staff	36,00	4	D-L2-08	karpet tile matte	cat matte krem	akustik panel
L2-GARDEN	Taman dalam	L2	recreation	staff	48,00	2	D-L2-09	deck komposit	panel tanaman	terbuka/pergola
L2-CORE	Inti tangga & lift L2	L2	circulation	staff	36,00	0	D-L2-10, D-L2-12	vinyl motif kayu	cat matte krem + panel kayu	gypsum
L2-GAME	Ruang game	L2	recreation	staff	72,00	8	D-L2-11, D-L2-19	vinyl motif kayu	cat matte krem + panel kayu	gypsum
L2-NCORR	Koridor utara L2	L2	circulation	staff	64,00	0	D-L2-12, D-L2-19, D-L2-13, D-L2-14, D-L2-15, D-L2-16, D-L2-18	vinyl motif kayu	cat matte krem + panel kayu	gypsum
L2-BALCONY	Balkon taman	L2	outdoor	staff	38,50	2	D-L2-13	deck komposit	panel tanaman	terbuka/pergola
L2-BILLIARD	Ruang biliar	L2	recreation	staff	38,50	0	D-L2-14	karpet tile matte	cat matte krem	akustik panel
L2-GYM	Ruang olahraga	L2	recreation	staff	49,50	3	D-L2-15	lantai karet olahraga	cat matte	akustik panel
L2-STORE	Gudang L2	L2	service	staff	33,00	0	D-L2-16	epoxy	cat matte	gypsum
L2-SERVICE	Area servis L2	L2	service	staff	16,50	0	D-L2-18	epoxy	cat matte	gypsum
Subtotal L2	17 ruang				768,00	42	cek: jumlah = envelope 768,00 m² COCOK			

- Sumber: tools/room_schedule.py atas design/world.json revisi P03; tabel dan subtotal dihitung saat render.
- Kursi = slot duduk dari fixture (AS-OCC-02), bukan target okupansi.
- Pemeriksaan: jumlah luas ruang per lantai harus sama dengan luas envelope; hasil tertulis di baris subtotal tiap lantai.
- Halaman 1 dari 2; schedule pintu dan jendela di halaman 2.

STATUS KONSEP — Bukan untuk konstruksi

kantor-rpg Proyek kantor-rpg · gedung KRPG-01

Room schedule, pintu dan jendela

Skala	NTS @ A3 lanskap
Revisi	P03 · 2026-10-01
Render	2026-10-13 01:12:51 UTC
Halaman	1/2
Digambar	Claude Code cloud (generator)
Diperiksa	Max (supervisor) belum review
Sumber	world.json sha256 38f94d70975b0c42

Huruf: Helvetica fallback (Alegreya Sans tidak tersedia saat build).

Nomor lembar

A-103

Rev P03 · 1/2

KONSEP — UNTUK DISKUSI

SCHEDULE PINTU DAN JENDELA

NTS · dari world.json doors[] dan windows[] revisi P03

ID pintu	Tag	Lantai	Ruang yang dihubungkan	Tipe	Lebar m	Buka ke	Engsel	Exit
D-L1-ENT	DENT	L1	EXT / L1-LOBBY	double	2	EXT (luar)	both (2 daun)	ya
D-L1-01	D1	L1	L1-LOBBY / L1-CORR	opening	3	-	-	
D-L1-02	D2	L1	L1-LOBBY / L1-MEET	double	1,8	L1-MEET	both (2 daun)	
D-L1-03	D3	L1	L1-MEET / L1-CORR	single	1	L1-MEET	low (barat)	
D-L1-04	D4	L1	L1-LOBBY / L1-GALLERY	opening	2,4	-	-	
D-L1-05	D5	L1	L1-GALLERY / L1-CORR	single	1	L1-GALLERY	low (barat)	
D-L1-06	D6	L1	L1-PANTRY / L1-CORR	single	1	L1-PANTRY	low (barat)	
D-L1-07	D7	L1	L1-WC / L1-CORR	single	1	L1-WC	low (barat)	
D-L1-08	D8	L1	L1-WC / L1-SHAFT-W	hatch	0,6	-	-	
D-L1-EXW	DEXW	L1	EXT / L1-CORR	single	1,2	EXT (luar)	low (selatan)	ya
D-L1-EXE	DEXE	L1	EXT / L1-CORR	single	1,2	EXT (luar)	low (selatan)	ya
D-L1-09	D9	L1	L1-CORR / L1-DISC	single	1	L1-DISC	low (barat)	
D-L1-10	D10	L1	L1-CORR / L1-IMPL	single	1	L1-IMPL	low (barat)	
D-L1-11	D11	L1	L1-CORR / L1-CORE	opening	2,4	-	-	
D-L1-12	D12	L1	L1-CORR / L1-NOVA	single	1	L1-NOVA	low (barat)	
D-L1-13	D13	L1	L1-CORR / L1-LAB	single	1	L1-LAB	low (barat)	
D-L1-14	D14	L1	L1-CORE / L1-NCORR	single	1	L1-NCORR	high (timur)	
D-L1-22	D22	L1	L1-LAB / L1-NCORR	single	1	L1-LAB	low (barat)	
D-L1-EXN	DEXN	L1	EXT / L1-NCORR	single	1,2	EXT (luar)	low (selatan)	ya
D-L1-15	D15	L1	L1-NCORR / L1-CEO	single	1	L1-CEO	low (barat)	
D-L1-16	D16	L1	L1-NCORR / L1-HUGO	single	1	L1-HUGO	low (barat)	
D-L1-17	D17	L1	L1-NCORR / L1-KEVIN	single	1	L1-KEVIN	low (barat)	
D-L1-18	D18	L1	L1-NCORR / L1-BRUNO	single	1	L1-BRUNO	low (barat)	
D-L1-19	D19	L1	L1-BRUNO / L1-SERVER	single	1	L1-SERVER	low (selatan)	
D-L1-21	D21	L1	L1-NCORR / L1-STORE	single	1	L1-STORE	high (timur)	
D-L2-01	D1	L2	L2-LOUNGE / L2-CORR	opening	3	-	-	
D-L2-02	D2	L2	L2-READ / L2-CORR	single	1	L2-READ	low (barat)	
D-L2-03	D3	L2	L2-DINE / L2-CORR	single	1,2	L2-DINE	low (barat)	
D-L2-04	D4	L2	L2-LOUNGE / L2-DINE	opening	2	-	-	
D-L2-05	D5	L2	L2-SHOWER / L2-CORR	single	1	L2-SHOWER	low (barat)	
D-L2-06	D6	L2	L2-WC / L2-CORR	single	1	L2-WC	low (barat)	
D-L2-07	D7	L2	L2-WC / L2-SHAFT-W	hatch	0,6	-	-	
D-L2-EXE	DEXE	L2	EXT / L2-CORR	single	1,2	EXT (luar)	low (selatan)	ya
D-L2-08	D8	L2	L2-CORR / L2-CHAT	single	1	L2-CHAT	low (barat)	
D-L2-09	D9	L2	L2-CORR / L2-GARDEN	opening	2	-	-	
D-L2-10	D10	L2	L2-CORR / L2-CORE	opening	2,4	-	-	
D-L2-11	D11	L2	L2-CORR / L2-GAME	double	1,6	L2-GAME	both (2 daun)	
D-L2-12	D12	L2	L2-CORE / L2-NCORR	single	1	L2-NCORR	high (timur)	
D-L2-19	D19	L2	L2-GAME / L2-NCORR	single	1	L2-GAME	low (barat)	
D-L2-13	D13	L2	L2-NCORR / L2-BALCONY	sliding	1,6	-	-	
D-L2-14	D14	L2	L2-NCORR / L2-BILLIARD	single	1,2	L2-BILLIARD	low (barat)	
D-L2-15	D15	L2	L2-NCORR / L2-GYM	double	1,6	L2-GYM	both (2 daun)	
D-L2-16	D16	L2	L2-NCORR / L2-STORE	single	1	L2-STORE	low (barat)	
D-L2-18	D18	L2	L2-NCORR / L2-SERVICE	single	1	L2-SERVICE	high (timur)	

ID jendela	Tag	Lantai	Ruang	Fasad	Lebar m	Ambang m	Kepala m	Kaca
W-L1-001	W1	L1	L1-MEET	S	1,5	0,9	2,4	bening
W-L1-002	W2	L1	L1-MEET	S	1,5	0,9	2,4	bening
W-L1-003	W3	L1	L1-MEET	W	1,5	0,9	2,4	bening
W-L1-004	W4	L1	L1-MEET	W	1,5	0,9	2,4	bening
W-L1-005	W5	L1	L1-LOBBY	S	1,5	0,9	2,4	bening
W-L1-006	W6	L1	L1-LOBBY	S	1,5	0,9	2,4	bening
W-L1-007	W7	L1	L1-PANTRY	S	0,9	1,6	2,4	buram
W-L1-008	W8	L1	L1-WC	E	0,9	1,6	2,4	buram
W-L1-009	W9	L1	L1-WC	E	0,9	1,6	2,4	buram
W-L1-010	W10	L1	L1-WC	E	0,9	1,6	2,4	buram
W-L1-011	W11	L1	L1-DISC	W	1,5	0,9	2,4	bening
W-L1-012	W12	L1	L1-CEO	N	1,5	0,9	2,4	bening
W-L1-013	W13	L1	L1-CEO	N	1,5	0,9	2,4	bening
W-L1-014	W14	L1	L1-HUGO	N	1,5	0,9	2,4	bening
W-L1-015	W15	L1	L1-HUGO	N	1,5	0,9	2,4	bening
W-L1-016	W16	L1	L1-KEVIN	N	1,5	0,9	2,4	bening
W-L1-017	W17	L1	L1-KEVIN	N	1,5	0,9	2,4	bening
W-L1-018	W18	L1	L1-BRUNO	N	1,5	0,9	2,4	bening
W-L1-019	W19	L1	L1-STORE	E	0,9	1,6	2,4	buram
W-L1-020	W20	L1	L1-STORE	E	0,9	1,6	2,4	buram
W-L2-021	W21	L2	L2-READ	S	1,5	0,9	2,4	bening
W-L2-022	W22	L2	L2-READ	S	1,5	0,9	2,4	bening
W-L2-023	W23	L2	L2-LOUNGE	S	1,5	0,9	2,4	bening
W-L2-024	W24	L2	L2-LOUNGE	S	1,5	0,9	2,4	bening
W-L2-025	W25	L2	L2-DINE	S	1,5	0,9	2,4	bening
W-L2-026	W26	L2	L2-DINE	S	1,5	0,9	2,4	bening
W-L2-027	W27	L2	L2-WC	E	0,9	1,6	2,4	buram
W-L2-028	W28	L2	L2-WC	E	0,9	1,6	2,4	buram
W-L2-029	W29	L2	L2-WC	E	0,9	1,6	2,4	buram
W-L2-030	W30	L2	L2-CHAT	W	1,5	0,9	2,4	bening
W-L2-031	W31	L2	L2-CHAT	W	1,5	0,9	2,4	bening
W-L2-032	W32	L2	L2-GAME	E	1,5	0,9	2,4	bening
W-L2-033	W33	L2	L2-BILLIARD	N	1,5	0,9	2,4	bening
W-L2-034	W34	L2	L2-BILLIARD	N	1,5	0,9	2,4	bening
W-L2-035	W35	L2	L2-GYM	N	1,5	0,9	2,4	bening
W-L2-036	W36	L2	L2-STORE	N	0,9	1,6	2,4	buram
W-L2-037	W37	L2	L2-STORE	N	0,9	1,6	2,4	buram
W-L2-038	W38	L2	L2-SERVICE	E	0,9	1,6	2,4	buram
W-L2-039	W39	L2	L2-SERVICE	E	0,9	1,6	2,4	buram

CATATAN SCHEDULE

- 44 pintu/bukaan (34 berdaun, data swing), 39 jendela (13 kaca buram).
- Tag = label di denah, tampak dan potongan. Jendela: W + nomor urut, unik untuk kedua lantai. Pintu: D + kode pintu pada lantainya (denah per lantai).
- Buka ke = ruang tempat daun berayun (swing.into). Engsel low/high = kusen di koordinat lebih kecil/besar sepanjang dinding; arah mata angin dalam kurung.
- Ambang dan kepala dari lantai jadi masing-masing (L1 ±0,00 m, L2 +4,00 m). Fasad S/E/N/W = selatan/timur/utara/barat (Y+ utara).
- Semua jendela konsep; kusen, material dan U-value belum didesain.

KONSEP · BUKAN UNTUK KONSTRUKSI

STATUS KONSEP — Bukan untuk konstruksi

kantor-rpg Proyek kantor-rpg · gedung KRPG-01

Room schedule, pintu dan jendela


Skala	NTS @ A3 lanskap
Revisi	P03 · 2026-10-01
Render	2026-10-13 01:12:51 UTC
Halaman	2/2
Digambar	Claude Code cloud (generator)
Diperiksa	Max (supervisor) belum review
Sumber	world.json sha256 38f94d70975b0c42

Huruf: Helvetica fallback (Alegreya Sans tidak tersedia saat build).

Nomor lembar

A-103

Rev P03 · 2/2

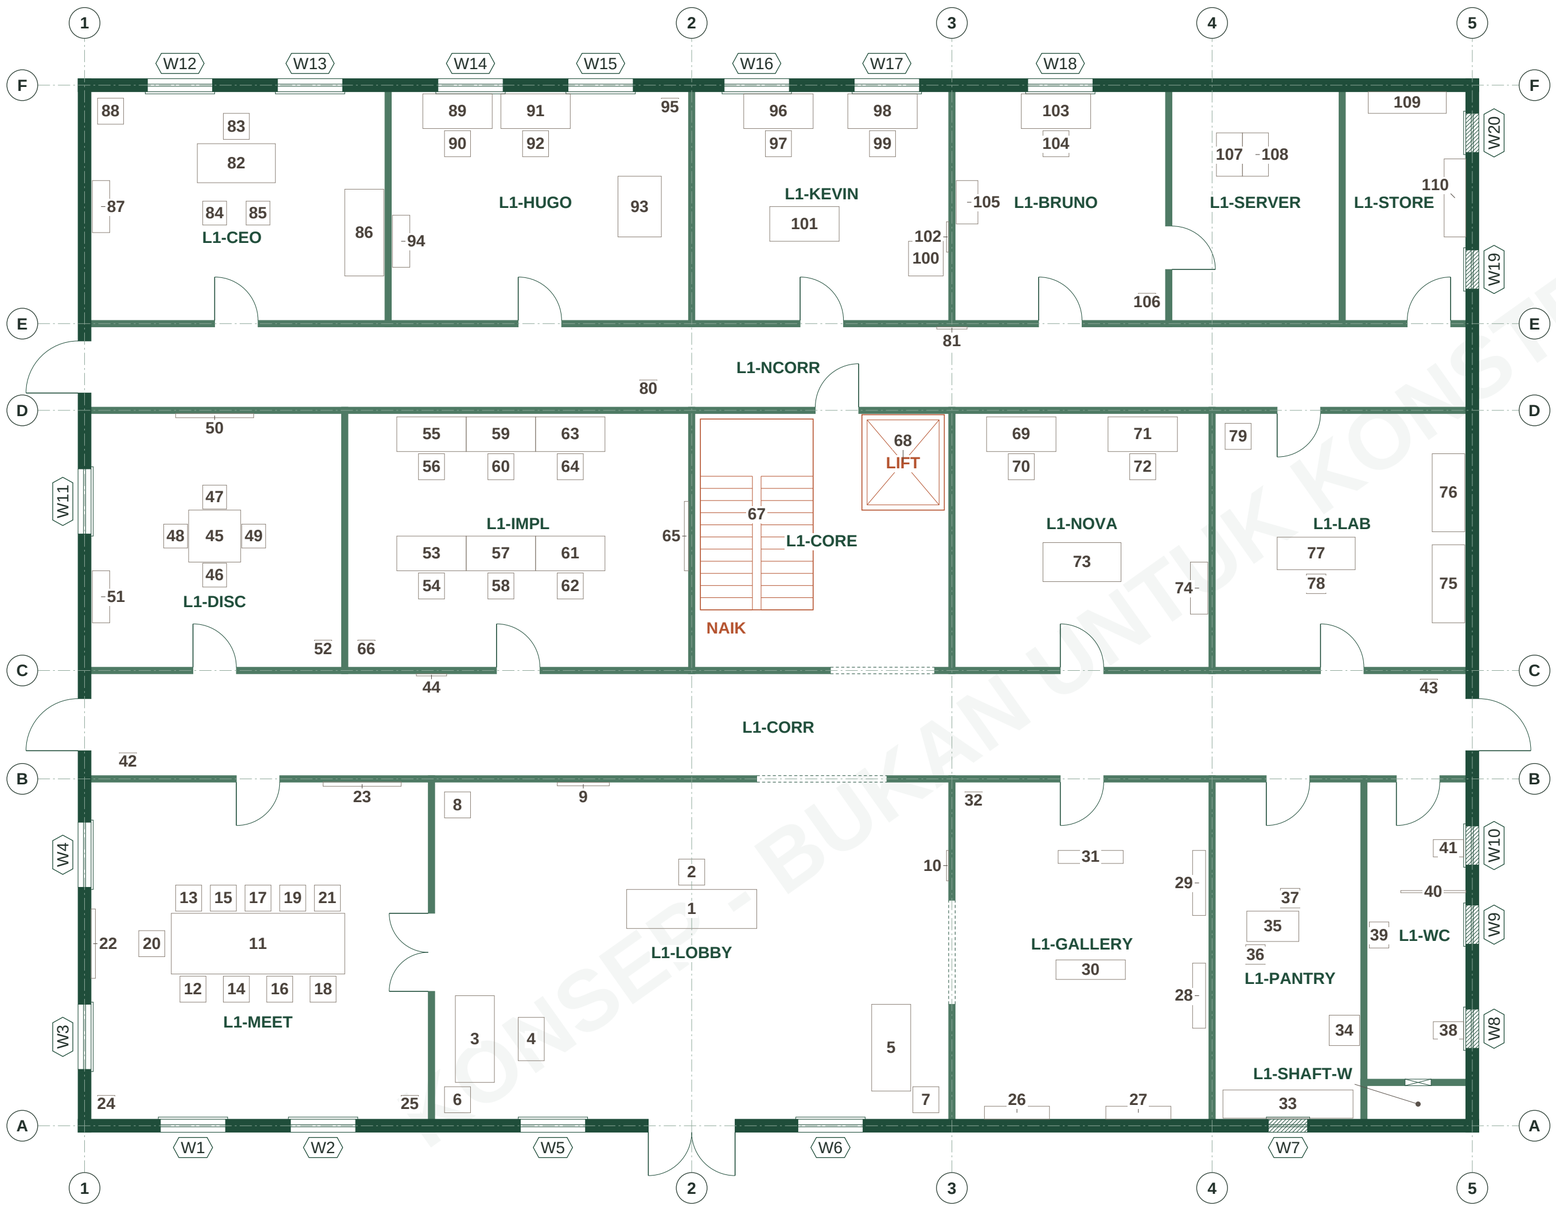

LAYOUT FURNITURE LANTAI 1 Skala 1:100 @ A2

Angka pada furniture = nomor fixture (FX-L1-nnn tanpa nol depan); ID lengkap di halaman 2. Segi enam Wnn = jendela (schedule A-103).

0 1 2 5 10 m (1:100)

U

Utara = sumbu Y+ dunia
Lantai L1: Lantai 1 - Kerja & Kunjungan
Ukuran furniture = target catalog (AS-DIM-04).

JENIS FIXTURE (37 jenis, 110 unit)

Jenis (catalog)	Ukuran m	n
Kursi kerja	0,6x0,6	25
Meja kerja + monitor	1,6x0,8	13
Tanaman kecil	0,4x0,4	10
Kursi tamu	0,55x0,55	6
Panel galeri	1,5x0,3	5
Tanaman besar	0,6x0,6	4
Poster/pamflet	0,7x0,05	4
Rak buku	1,2x0,4	3
Meja lab ICT	1,8x0,75	3
Sofa	2x0,9	3
Bangku tinggi	0,45x0,45	3
Rack 42U (target)	0,6x1	2
Rak gudang	1,8x0,5	2
Layar dinding	1,6x0,1	2
Kloset	0,4x0,7	2
Papan tulis	1,8x0,1	2
Bangku	1,6x0,45	1
Meja kopi	1x0,6	1
Meja CEO	1,8x0,9	1
Papan direktori	1,2x0,08	1
Meja gambar	1,4x1	1
Easel	0,8x0,8	1
Kulkas	0,7x0,7	1
Meja tinggi	1,2x0,7	1
Rack lab terbuka 12U	0,6x0,6	1
Lift (konsep)	1,9x2,2	1
Meja rapat	4x1,4	1
Rak model	1,2x0,4	1
Counter pantry	3x0,65	1
Partisi bilik	1,5x0,05	1
Meja denah (blueprint)	1,8x0,9	1
Meja resepsi	3x0,9	1
Meja bundar	1,2x1,2	1
Wastafel	0,6x0,45	1
Tangga U (konsep)	2,6x4,4	1
Lemari alat	1x0,5	1
Meja kerja berdiri	1,6x0,8	1

Nomor kunci per fixture dan ruangnya: halaman 2.

STATUS KONSEP Bukan untuk konstruksi

kantor-rpg Proyek kantor-rpg · gedung KRPG-01

Layout furniture Lantai 1

Skala	1:100 @ A2 lanskap
Revisi	P03 · 2026-10-01
Render	2026-10-13 01:12:51 UTC
Halaman	1/2
Digambar	Claude Code cloud (generator)
Diperiksa	Max (supervisor) belum review
Sumber	world.json sha256 38f94d70975b0c42

Nomor lembar
A-201
Rev P03 · 1/2

Huruf: Helvetica fallback (Alegreya Sans tidak tersedia saat build).

BUKAN UNTUK KONSTRUKSI

DAFTAR FIXTURE L1 (nomor kunci di denah halaman 1)

110 fixture dari world.json revisi P03

No	ID	Jenis	Ruang
1	FX-L1-001	Meja resepsi	LOBBY
2	FX-L1-002	Kursi kerja	LOBBY
3	FX-L1-003	Sofa	LOBBY
4	FX-L1-004	Meja kopi	LOBBY
5	FX-L1-005	Sofa	LOBBY
6	FX-L1-006	Tanaman besar	LOBBY
7	FX-L1-007	Tanaman besar	LOBBY
8	FX-L1-008	Tanaman besar	LOBBY
9	FX-L1-009	Papan direktori	LOBBY
10	FX-L1-010	Poster/pamflet	LOBBY
11	FX-L1-011	Meja rapat	MEET
12	FX-L1-012	Kursi kerja	MEET
13	FX-L1-013	Kursi kerja	MEET
14	FX-L1-014	Kursi kerja	MEET
15	FX-L1-015	Kursi kerja	MEET
16	FX-L1-016	Kursi kerja	MEET
17	FX-L1-017	Kursi kerja	MEET
18	FX-L1-018	Kursi kerja	MEET
19	FX-L1-019	Kursi kerja	MEET
20	FX-L1-020	Kursi kerja	MEET
21	FX-L1-021	Kursi kerja	MEET
22	FX-L1-022	Layar dinding	MEET
23	FX-L1-023	Papan tulis	MEET
24	FX-L1-024	Tanaman kecil	MEET
25	FX-L1-025	Tanaman kecil	MEET
26	FX-L1-026	Panel galeri	GALLERY
27	FX-L1-027	Panel galeri	GALLERY
28	FX-L1-028	Panel galeri	GALLERY
29	FX-L1-029	Panel galeri	GALLERY
30	FX-L1-030	Bangku	GALLERY
31	FX-L1-031	Panel galeri	GALLERY
32	FX-L1-032	Tanaman kecil	GALLERY
33	FX-L1-033	Counter pantry	PANTRY
34	FX-L1-034	Kulkas	PANTRY
35	FX-L1-035	Meja tinggi	PANTRY
36	FX-L1-036	Bangku tinggi	PANTRY
37	FX-L1-037	Bangku tinggi	PANTRY
38	FX-L1-038	Kloset	WC
39	FX-L1-039	Wastafel	WC
40	FX-L1-040	Partisi bilik	WC
41	FX-L1-041	Kloset	WC
42	FX-L1-042	Tanaman kecil	CORR
43	FX-L1-043	Tanaman kecil	CORR
44	FX-L1-044	Poster/pamflet	CORR
45	FX-L1-045	Meja bundar	DISC
46	FX-L1-046	Kursi tamu	DISC
47	FX-L1-047	Kursi tamu	DISC
48	FX-L1-048	Kursi tamu	DISC
49	FX-L1-049	Kursi tamu	DISC
50	FX-L1-050	Papan tulis	DISC
51	FX-L1-051	Rak buku	DISC
52	FX-L1-052	Tanaman kecil	DISC
53	FX-L1-053	Meja kerja + monitor	IMPL
54	FX-L1-054	Kursi kerja	IMPL
55	FX-L1-055	Meja kerja + monitor	IMPL
56	FX-L1-056	Kursi kerja	IMPL
57	FX-L1-057	Meja kerja + monitor	IMPL
58	FX-L1-058	Kursi kerja	IMPL
59	FX-L1-059	Meja kerja + monitor	IMPL
60	FX-L1-060	Kursi kerja	IMPL
61	FX-L1-061	Meja kerja + monitor	IMPL
62	FX-L1-062	Kursi kerja	IMPL
63	FX-L1-063	Meja kerja + monitor	IMPL
64	FX-L1-064	Kursi kerja	IMPL
65	FX-L1-065	Layar dinding	IMPL
66	FX-L1-066	Tanaman kecil	IMPL
67	FX-L1-067	Tangga U (konsep)	CORE
68	FX-L1-068	Lift (konsep)	CORE
69	FX-L1-069	Meja kerja + monitor	NOVA
70	FX-L1-070	Kursi kerja	NOVA
71	FX-L1-071	Meja kerja + monitor	NOVA
72	FX-L1-072	Kursi kerja	NOVA
73	FX-L1-073	Meja denah (blueprint)	NOVA
74	FX-L1-074	Rak buku	NOVA
75	FX-L1-075	Meja lab ICT	LAB
76	FX-L1-076	Meja lab ICT	LAB
77	FX-L1-077	Meja lab ICT	LAB
78	FX-L1-078	Bangku tinggi	LAB
79	FX-L1-079	Rack lab terbuka 12U	LAB
80	FX-L1-080	Tanaman kecil	NCORR
81	FX-L1-081	Poster/pamflet	NCORR
82	FX-L1-082	Meja CEO	CEO
83	FX-L1-083	Kursi kerja	CEO
84	FX-L1-084	Kursi tamu	CEO
85	FX-L1-085	Kursi tamu	CEO
86	FX-L1-086	Sofa	CEO
87	FX-L1-087	Rak buku	CEO
88	FX-L1-088	Tanaman besar	CEO
89	FX-L1-089	Meja kerja + monitor	HUGO
90	FX-L1-090	Kursi kerja	HUGO
91	FX-L1-091	Meja kerja + monitor	HUGO
92	FX-L1-092	Kursi kerja	HUGO
93	FX-L1-093	Meja gambar	HUGO
94	FX-L1-094	Rak model	HUGO
95	FX-L1-095	Tanaman kecil	HUGO
96	FX-L1-096	Meja kerja + monitor	KEVIN
97	FX-L1-097	Kursi kerja	KEVIN
98	FX-L1-098	Meja kerja + monitor	KEVIN
99	FX-L1-099	Kursi kerja	KEVIN
100	FX-L1-100	Easel	KEVIN
101	FX-L1-101	Meja kerja berdiri	KEVIN
102	FX-L1-102	Poster/pamflet	KEVIN
103	FX-L1-103	Meja kerja + monitor	BRUNO
104	FX-L1-104	Kursi kerja	BRUNO
105	FX-L1-105	Lemari alat	BRUNO
106	FX-L1-106	Tanaman kecil	BRUNO
107	FX-L1-107	Rack 42U (target)	SERVER
108	FX-L1-108	Rack 42U (target)	SERVER
109	FX-L1-109	Rak gudang	STORE
110	FX-L1-110	Rak gudang	STORE

KONSEP - BUKAN UNTUK KONSTRUKSI

STATUS KONSEP — Bukan untuk konstruksi

kantor-rpg Proyek kantor-rpg · gedung KRPG-01

Layout furniture Lantai 1


Skala	1:100 @ A2 lanskap
Revisi	P03 · 2026-10-01
Render	2026-10-13 01:12:51 UTC
Halaman	2/2
Digambar	Claude Code cloud (generator)
Diperiksa	Max (supervisor) belum review
Sumber	world.json sha256 38f94d70975b0c42

Huruf: Helvetica fallback (Alegreya Sans tidak tersedia saat build).

Nomor lembar

A-201

Rev P03 · 2/2

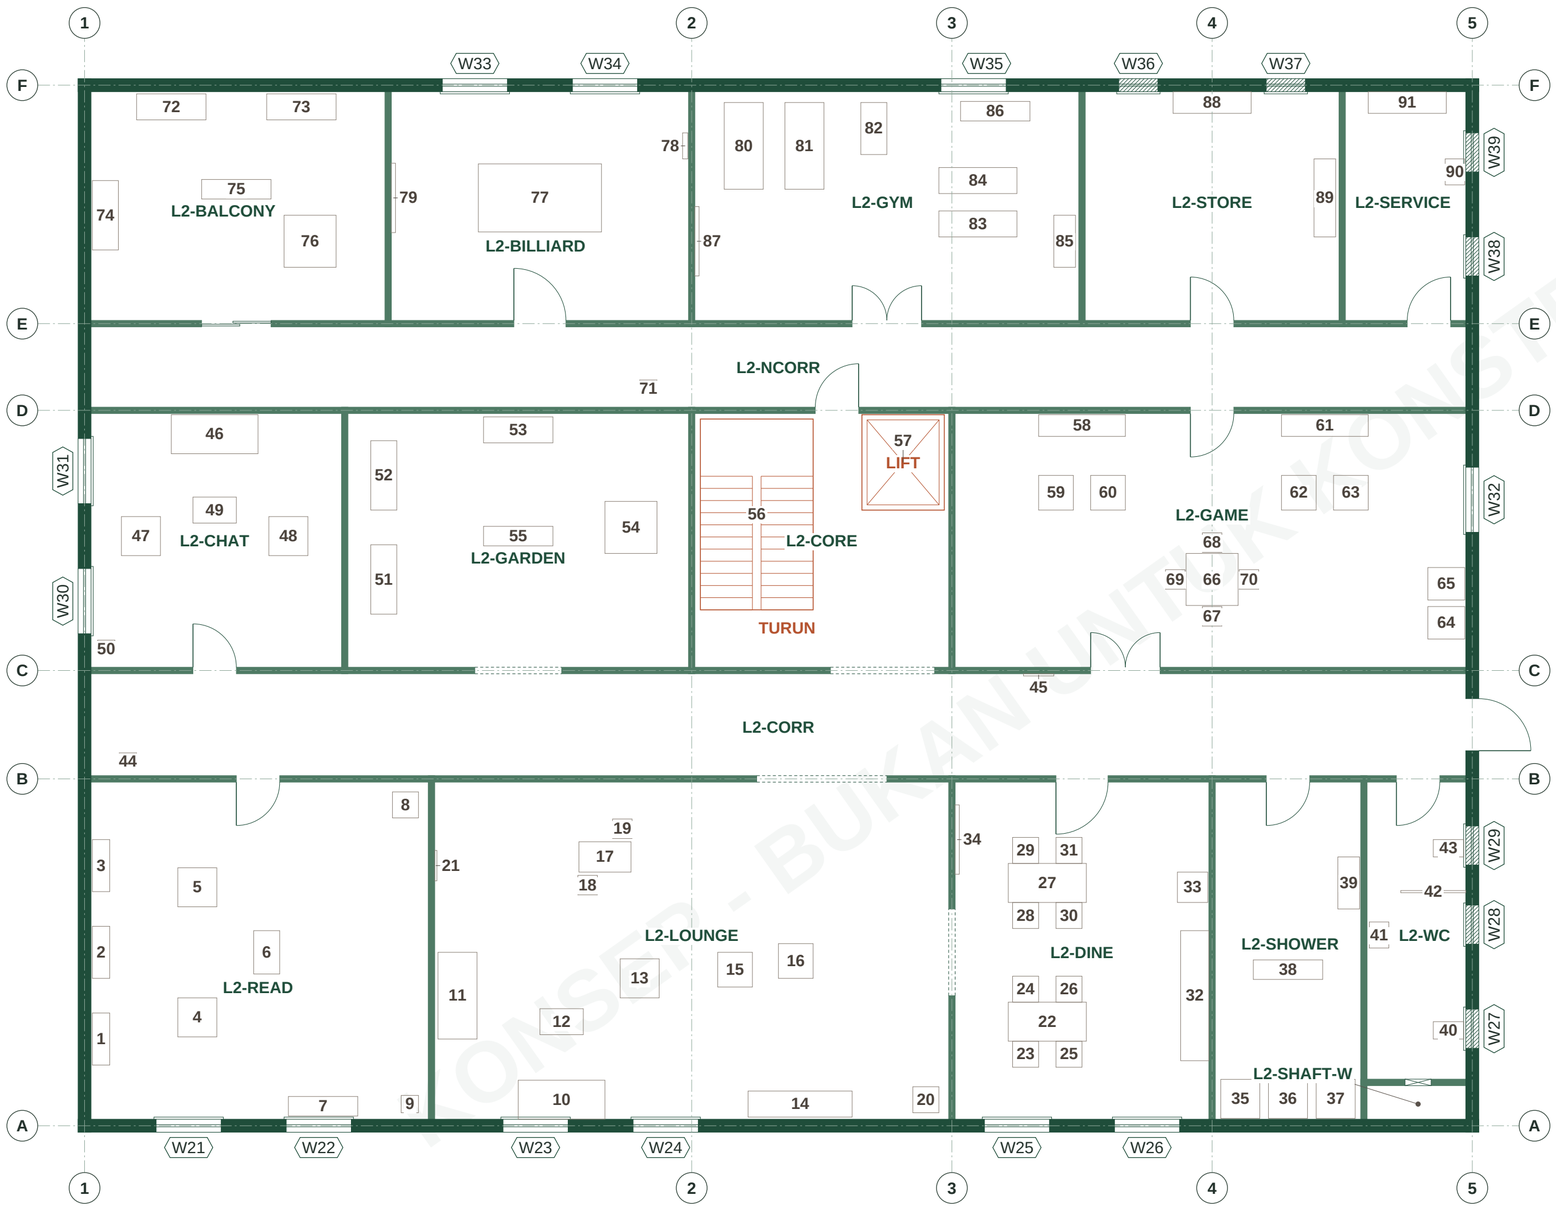

LAYOUT FURNITURE LANTAI 2 Skala 1:100 @ A2

Angka pada furniture = nomor fixture (FX-L2-nnn tanpa nol depan); ID lengkap di halaman 2. Segi enam Wnn = jendela (schedule A-103).

0 1 2 5 10 m (1:100)

U

Utara = sumbu Y+ dunia

Lantai L2: Lantai 2 - Rekreasi

Ukuran furniture = target catalog (AS-DIM-04).

JENIS FIXTURE (37 jenis, 91 unit)

Jenis (catalog)	Ukuran m	n
Kursi kerja	0,6x0,6	8
Beanbag	0,8x0,8	6
Planter	1,6x0,6	6
Bangku tinggi	0,45x0,45	6
Kursi santai	0,9x0,9	5
Bangku	1,6x0,45	5
Tanaman kecil	0,4x0,4	4
Rak buku	1,2x0,4	3
Meja kopi	1x0,6	3
Bilik shower	0,9x0,9	3
Sofa	2x0,9	3
Rak gudang	1,8x0,5	3
Layar dinding	1,6x0,1	3
Kabinet arcade	0,75x0,85	2
Meja makan	1,8x0,9	2
Matras	1,8x0,6	2
Konsol game + layar	2x0,5	2
Tanaman besar	0,6x0,6	2
Poster/pamflet	0,7x0,05	2
Wastafel	0,6x0,45	2
Treadmill	0,9x2	2
Kloset	0,4x0,7	2
Meja biliar 9 ft	2,84x1,57	1
Meja board game	1,2x1,2	1
Coffee bar	2,4x0,6	1
Rak stik	0,6x0,12	1
Rak dumbbell	1,2x0,5	1
Sepeda statis	0,6x1,2	1
Kulkas	0,7x0,7	1
Meja tinggi	1,2x0,7	1
Lift (konsep)	1,9x2,2	1
Loker	1,2x0,5	1
Counter pantry	3x0,65	1
Partisi bilik	1,5x0,05	1
Meja bundar	1,2x1,2	1
Tangga U (konsep)	2,6x4,4	1
Pohon dalam pot	1,2x1,2	1

Nomor kunci per fixture dan ruangnya: halaman 2.

STATUS KONSEP Bukan untuk konstruksi

kantor-rpg Proyek kantor-rpg · gedung KRPG-01

Layout furniture Lantai 2

Skala	1:100 @ A2 lanskap
Revisi	P03 · 2026-10-01
Render	2026-10-13 01:12:51 UTC
Halaman	1/2
Digambar	Claude Code cloud (generator)
Diperiksa	Max (supervisor) belum review
Sumber	world.json sha256 38f94d70975b0c42

Nomor lembar

A-202

Rev P03 · 1/2

Huruf: Helvetica fallback (Alegreya Sans tidak tersedia saat build).

KONSEP - BUKAN UNTUK KONSTRUKSI

DAFTAR FIXTURE L2 (nomor kunci di denah halaman 1)

91 fixture dari world.json revisi P03

No	ID	Jenis	Ruang
1	FX-L2-001	Rak buku	READ
2	FX-L2-002	Rak buku	READ
3	FX-L2-003	Rak buku	READ
4	FX-L2-004	Kursi santai	READ
5	FX-L2-005	Kursi santai	READ
6	FX-L2-006	Meja kopi	READ
7	FX-L2-007	Bangku	READ
8	FX-L2-008	Tanaman besar	READ
9	FX-L2-009	Tanaman kecil	READ
10	FX-L2-010	Sofa	LOUNGE
11	FX-L2-011	Sofa	LOUNGE
12	FX-L2-012	Meja kopi	LOUNGE
13	FX-L2-013	Kursi santai	LOUNGE
14	FX-L2-014	Coffee bar	LOUNGE
15	FX-L2-015	Beanbag	LOUNGE
16	FX-L2-016	Beanbag	LOUNGE
17	FX-L2-017	Meja tinggi	LOUNGE
18	FX-L2-018	Bangku tinggi	LOUNGE
19	FX-L2-019	Bangku tinggi	LOUNGE
20	FX-L2-020	Tanaman besar	LOUNGE
21	FX-L2-021	Poster/pamflet	LOUNGE
22	FX-L2-022	Meja makan	DINE
23	FX-L2-023	Kursi kerja	DINE
24	FX-L2-024	Kursi kerja	DINE
25	FX-L2-025	Kursi kerja	DINE
26	FX-L2-026	Kursi kerja	DINE
27	FX-L2-027	Meja makan	DINE
28	FX-L2-028	Kursi kerja	DINE
29	FX-L2-029	Kursi kerja	DINE
30	FX-L2-030	Kursi kerja	DINE
31	FX-L2-031	Kursi kerja	DINE
32	FX-L2-032	Counter pantry	DINE
33	FX-L2-033	Kulkas	DINE
34	FX-L2-034	Layar dinding	DINE
35	FX-L2-035	Bilik shower	SHOWER
36	FX-L2-036	Bilik shower	SHOWER
37	FX-L2-037	Bilik shower	SHOWER
38	FX-L2-038	Bangku	SHOWER
39	FX-L2-039	Loker	SHOWER
40	FX-L2-040	Kloset	WC
41	FX-L2-041	Wastafel	WC
42	FX-L2-042	Partisi bilik	WC
43	FX-L2-043	Kloset	WC
44	FX-L2-044	Tanaman kecil	CORR
45	FX-L2-045	Poster/pamflet	CORR
46	FX-L2-046	Sofa	CHAT
47	FX-L2-047	Kursi santai	CHAT
48	FX-L2-048	Kursi santai	CHAT
49	FX-L2-049	Meja kopi	CHAT
50	FX-L2-050	Tanaman kecil	CHAT
51	FX-L2-051	Planter	GARDEN
52	FX-L2-052	Planter	GARDEN
53	FX-L2-053	Planter	GARDEN
54	FX-L2-054	Pohon dalam pot	GARDEN
55	FX-L2-055	Bangku	GARDEN
56	FX-L2-056	Tangga U (konsep)	CORE
57	FX-L2-057	Lift (konsep)	CORE
58	FX-L2-058	Konsol game + layar	GAME
59	FX-L2-059	Beanbag	GAME
60	FX-L2-060	Beanbag	GAME
61	FX-L2-061	Konsol game + layar	GAME
62	FX-L2-062	Beanbag	GAME
63	FX-L2-063	Beanbag	GAME
64	FX-L2-064	Kabinet arcade	GAME
65	FX-L2-065	Kabinet arcade	GAME
66	FX-L2-066	Meja board game	GAME
67	FX-L2-067	Bangku tinggi	GAME
68	FX-L2-068	Bangku tinggi	GAME
69	FX-L2-069	Bangku tinggi	GAME
70	FX-L2-070	Bangku tinggi	GAME
71	FX-L2-071	Tanaman kecil	NCORR
72	FX-L2-072	Planter	BALCONY
73	FX-L2-073	Planter	BALCONY
74	FX-L2-074	Planter	BALCONY
75	FX-L2-075	Bangku	BALCONY
76	FX-L2-076	Meja bundar	BALCONY
77	FX-L2-077	Meja biliar 9 ft	BILLIARD
78	FX-L2-078	Rak stik	BILLIARD
79	FX-L2-079	Layar dinding	BILLIARD
80	FX-L2-080	Treadmill	GYM
81	FX-L2-081	Treadmill	GYM
82	FX-L2-082	Sepeda statis	GYM
83	FX-L2-083	Matras	GYM
84	FX-L2-084	Matras	GYM
85	FX-L2-085	Rak dumbbell	GYM
86	FX-L2-086	Bangku	GYM
87	FX-L2-087	Layar dinding	GYM
88	FX-L2-088	Rak gudang	STORE
89	FX-L2-089	Rak gudang	STORE
90	FX-L2-090	Wastafel	SERVICE
91	FX-L2-091	Rak gudang	SERVICE

KONSEP - BUKAN UNTUK KONSTRUKSI

STATUS KONSEP — Bukan untuk konstruksi

kantor-rpg Proyek kantor-rpg · gedung KRPG-01

Layout furniture Lantai 2

Skala	1:100 @ A2 lanskap
Revisi	P03 · 2026-10-01
Render	2026-10-13 01:12:51 UTC
Halaman	2/2
Digambar	Claude Code cloud (generator)
Diperiksa	Max (supervisor) belum review
Sumber	world.json sha256 38f94d70975b0c42


Huruf: Helvetica fallback (Alegreya Sans tidak tersedia saat build).

Nomor lembar

A-202


Rev P03 · 2/2

TAMPAK SELATAN 1:200

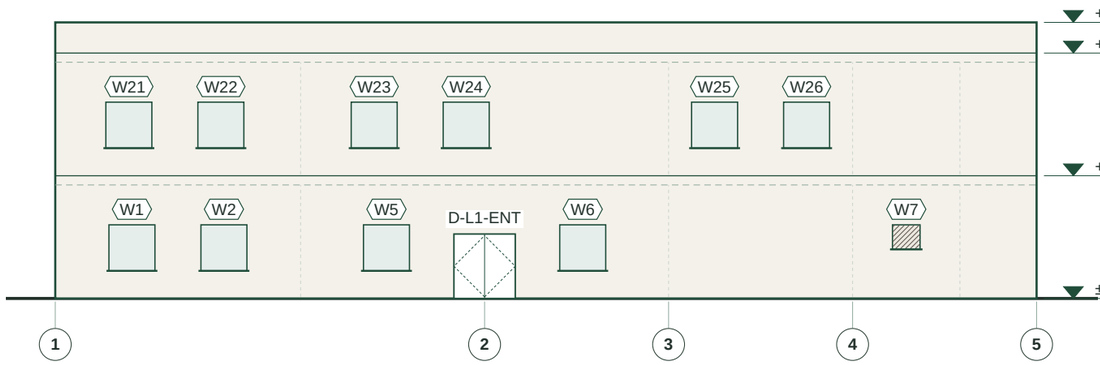

Panjang fasad 32 m, as ke as dinding luar.

TAMPAK UTARA 1:200

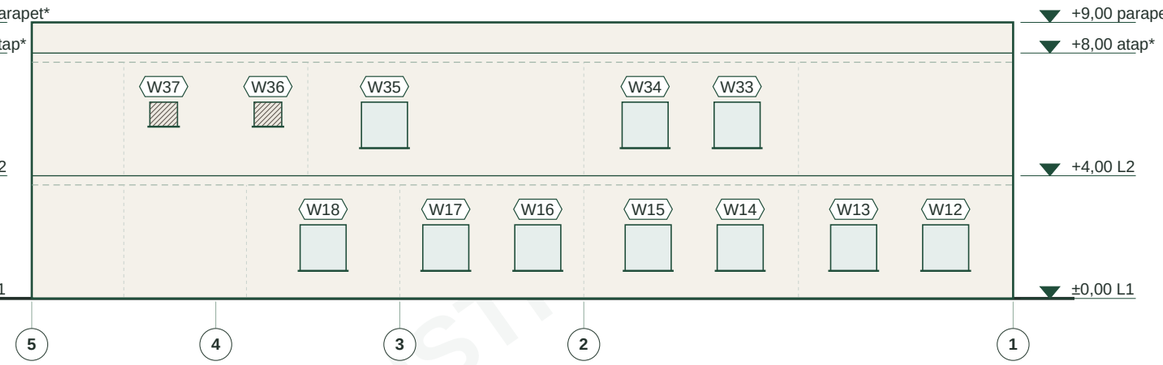


Panjang fasad 32 m, as ke as dinding luar.

TAMPAK TIMUR 1:200



Panjang fasad 24 m, as ke as dinding luar.

TAMPAK BARAT 1:200

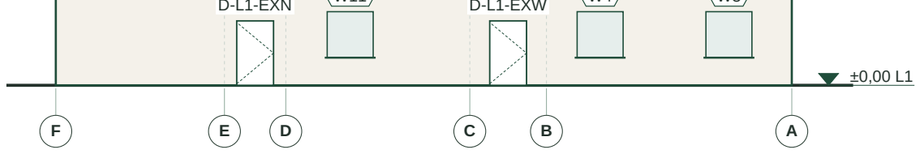

Panjang fasad 24 m, as ke as dinding luar.

CATATAN TAMPAK

- Tinggi antar lantai 4 m dan pelat 0,3 m dari world.json (AS-DIM-01, AS-DIM-03).
- * Atap dan parapet 1 m serta tinggi pintu 2,1 m adalah asumsi lembar ini (konsep); tidak ada di world.json.
- Jendela dari world.json windows (39 buah): posisi, lebar, ambang dan kepala per lantai; kaca buram diarsir. Kusen dan material fasad belum didesain.
- Tag segi enam Wnn = jendela nomor nn (W16 = W-L1-016); pasangan tag dan ID lengkap di schedule A-103 halaman 2.
- Segitiga putus pada pintu = sisi engsel (puncak segitiga) dari doors[].swing.hinge.
- Garis putus tipis = posisi dinding dalam yang bertemu fasad; garis putus abu = pelat tersembunyi.
- Pintu exit L2 timur menuju tangga darurat konsep VL-ESC-E di luar envelope (AS-EXIT-01), tidak digambar.

0 2 5 10 m (1:200)

STATUS KONSEP — Bukan untuk konstruksi

kantor-rpg Proyek kantor-rpg · gedung KRPG-01

Tampak

Skala	1:200 @ A3 lanskap
Revisi	P03 · 2026-10-01
Render	2026-10-13 01:12:51 UTC
Halaman	1/1
Digambar	Claude Code cloud (generator)
Diperiksa	Max (supervisor) belum review
Sumber	world.json sha256 38f94d70975b0c42

Huruf: Helvetica fallback (Alegreya Sans tidak tersedia saat build).

Nomor lembar


A-301

Rev P03 · 1/1

KONSEP - BUKAN UNTUK KONSTRUKSI


POTONGAN A-A

1:100 · memanjang (sumbu X) di y = 13,0 m melalui inti tangga dan lift

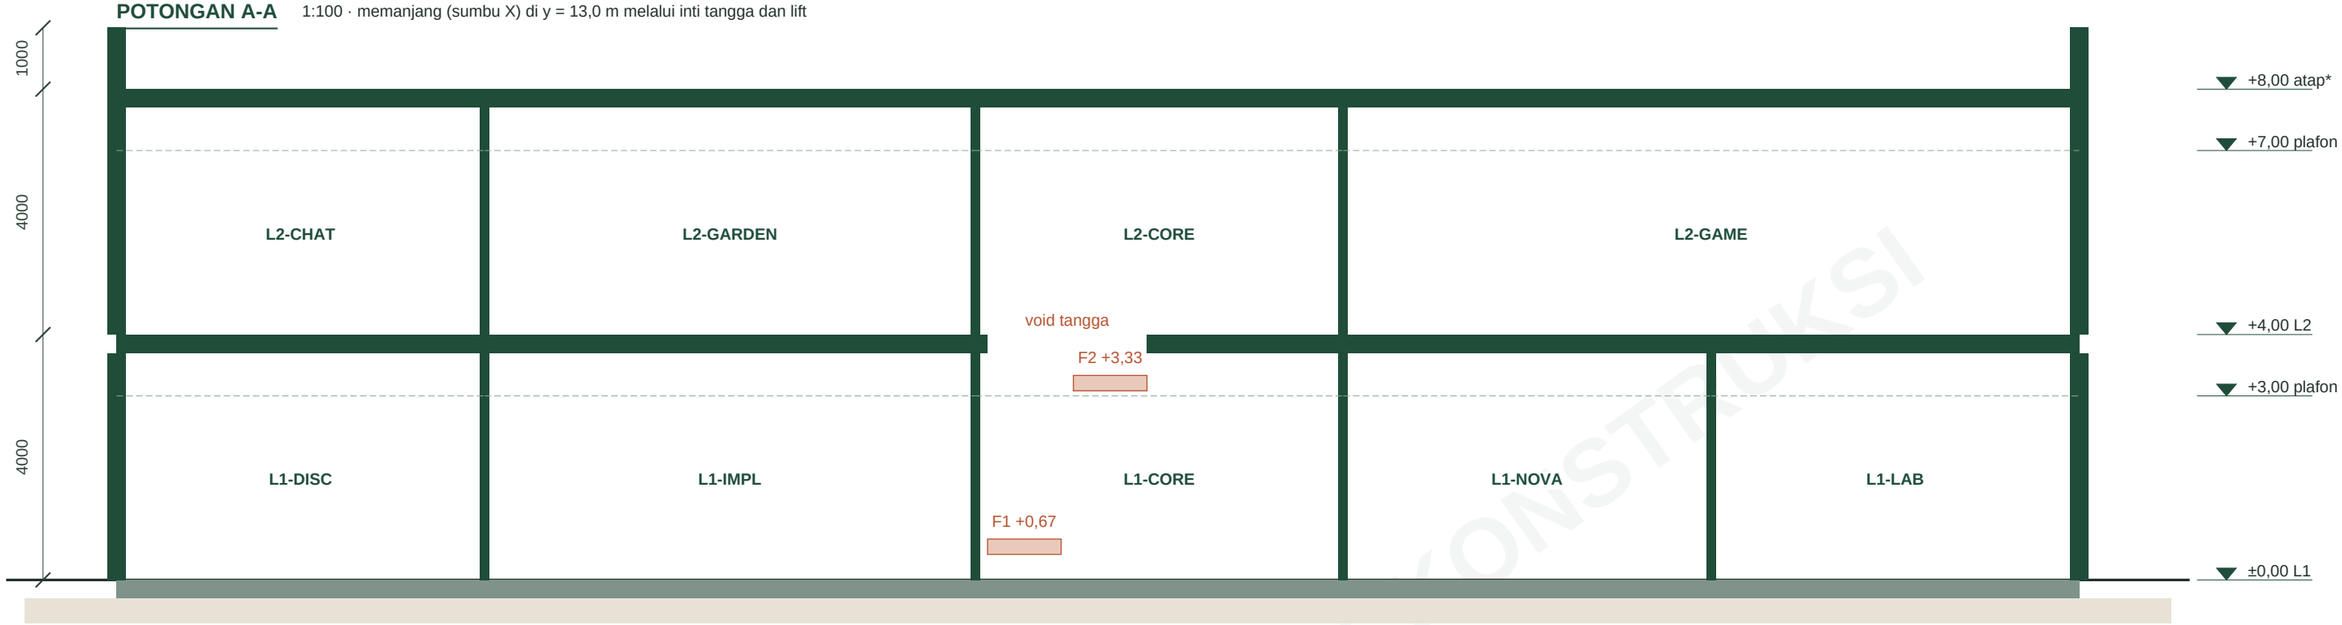


POTONGAN B-B

1:100 · melintang (sumbu Y) di x = 14,8 m melalui flight 1 tangga dan entrance

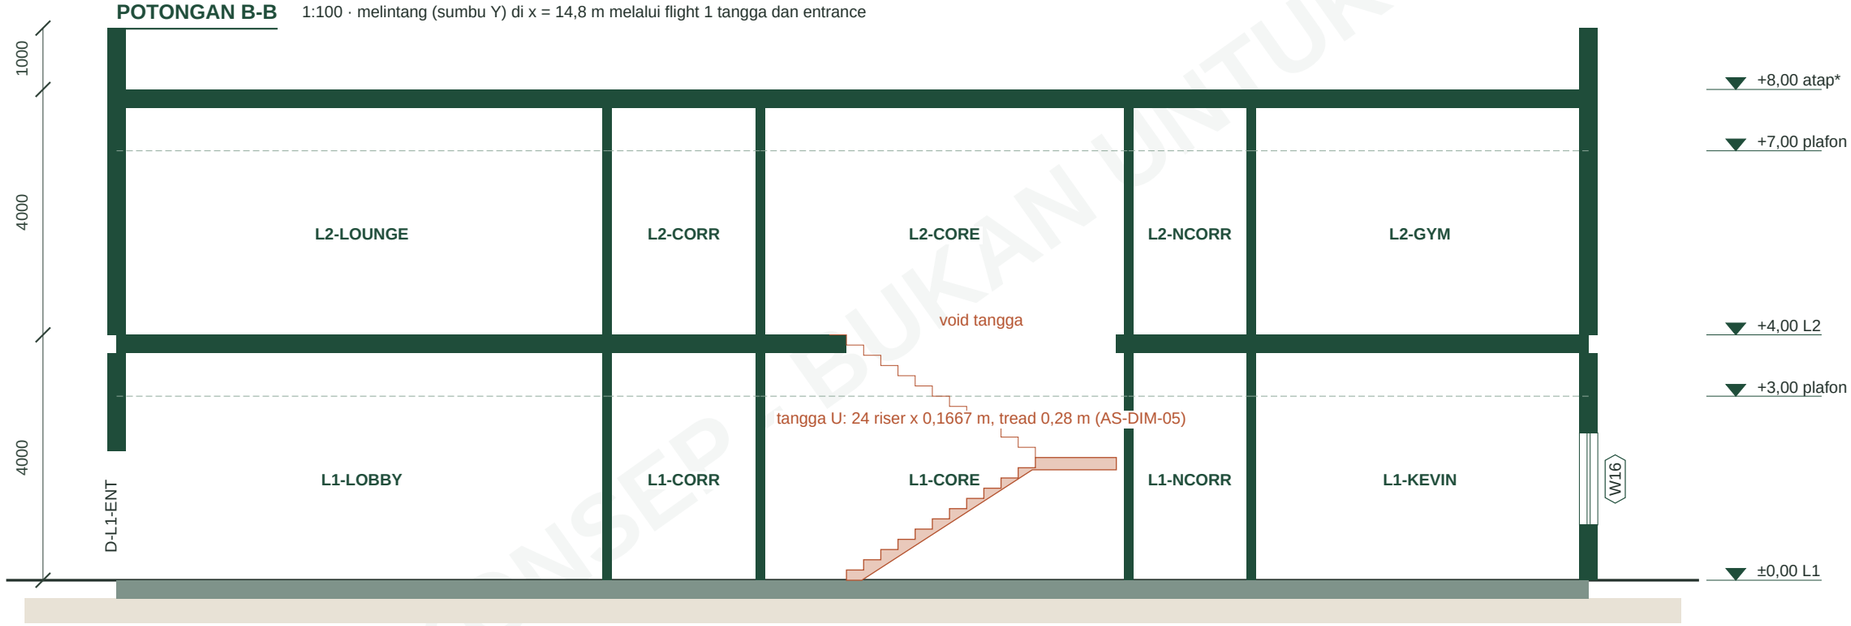

KUNCI POTONGAN L1 (1:500)

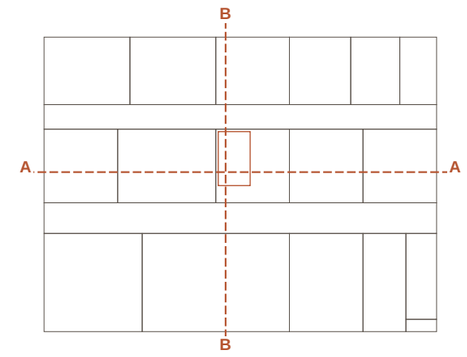

- Diturunkan dari world.json: tinggi antar lantai 4 m, plafon 3 m, pelat 0,3 m (AS-DIM-03); dinding dan bukaan dari derive_walls; tangga dari fixture stair_u (AS-DIM-05).
- Tinggi kepala pintu 2,1 m, parapet 1 m dan * atap konsep adalah asumsi lembar, bukan data world.json. Belum ada desain struktur atau fondasi.
- Hijau penuh = elemen terpotong (dinding, pelat). Garis putus = plafon. Terakota = tangga.
- Jendela yang terpotong garis potong digambar dengan ambang dan kepala dari world.json windows: W-L1-016 (tag W16).

STATUS KONSEP — Bukan untuk konstruksi

kantor-rpg Proyek kantor-rpg · gedung KRPG-01

Potongan

Skala	1:100 @ A3 lanskap
Revisi	P03 · 2026-10-01
Render	2026-10-13 01:12:51 UTC
Halaman	1/1
Digambar	Claude Code cloud (generator)
Diperiksa	Max (supervisor) belum review
Sumber	world.json sha256 38f94d70975b0c42

Huruf: Helvetica fallback (Alegreya Sans tidak tersedia saat build).

Nomor lembar

A-401

Rev P03 · 1/1

KONSEP — BUKAN UNTUK KONSTRUKSI