
TOPOLOGI JARINGAN (VIRTUAL)

RANCANGAN VIRTUAL, BUKAN TOPOLOGI PRODUKSI

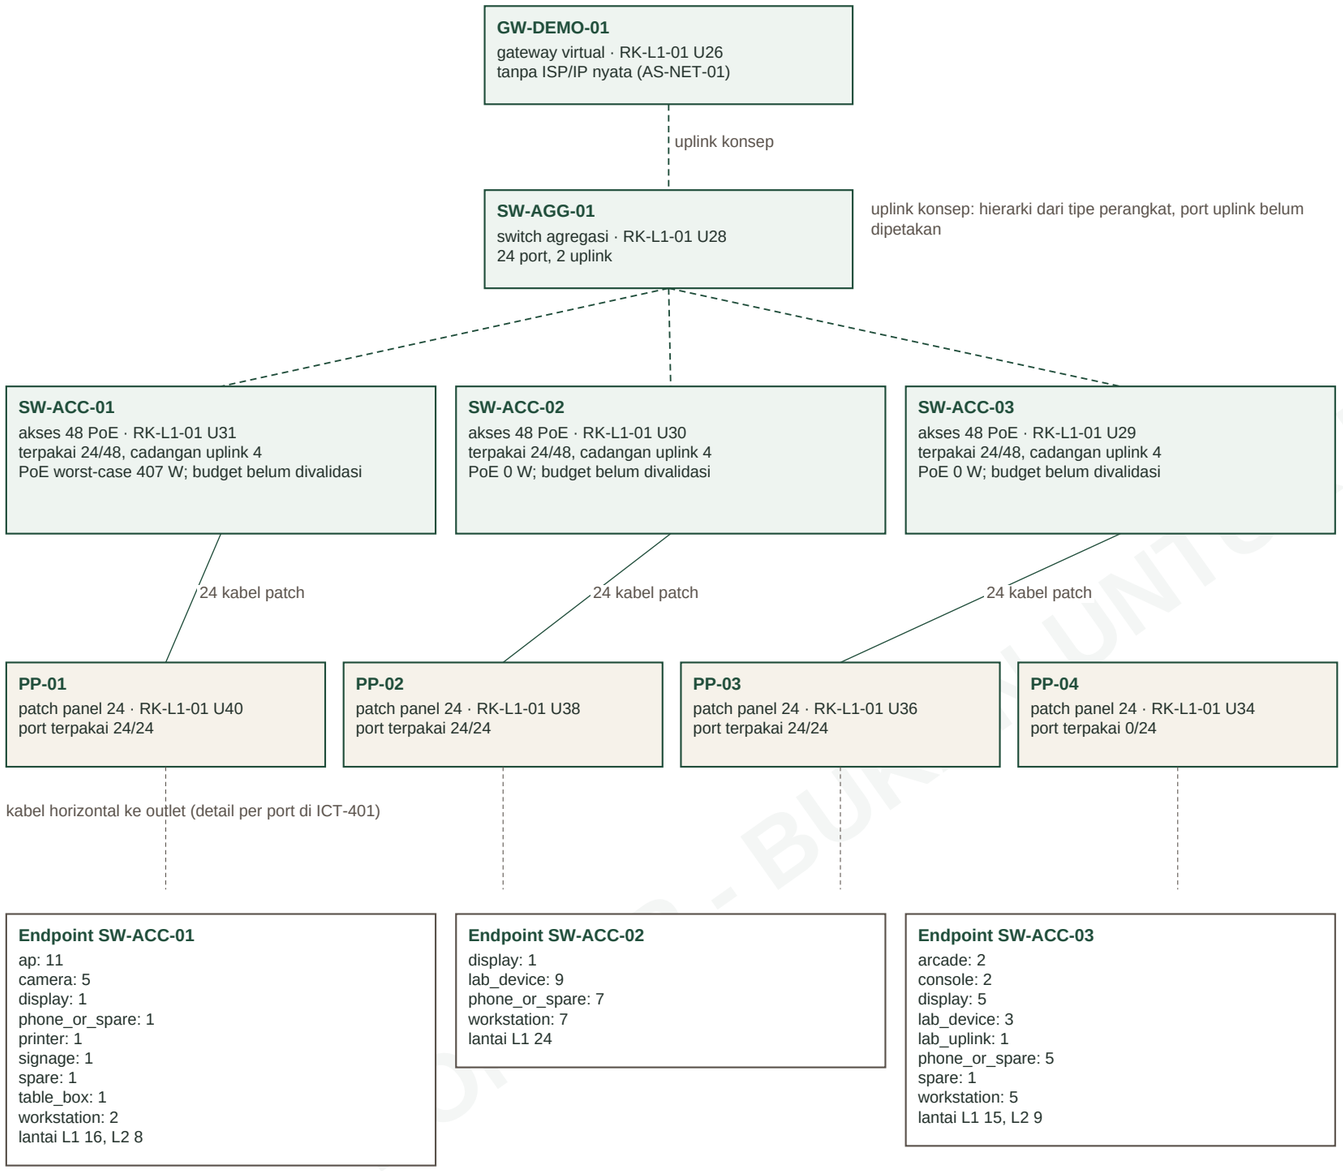

DOMAIN (ID abstrak, AS-NET-01)

Domain	Label	Port	Catatan
NET-OFFICE	office	48	abstrak
NET-DEMO	demo	10	abstrak
NET-GUEST	guest	0	abstrak, SSID tamu konsep
NET-LAB	lab	14	abstrak, terisolasi konsep
NET-SERVER	server	0	abstrak

JUMLAH DARI DATA

Outlet	45 outlet, 72 port
Patch panel	4 x 24 = 96 port, terpakai 72
Access point	11 placeholder (AS-ICT-01): L1 5, L2 6
Kamera	5 opsional konsep: L1 3, L2 2
Kabel	72 kabel, total 2074,8 m (AS-ICT-02)
PoE	worst-case 407 W dari kelas IEEE (AS-ICT-04); belum divalidasi

RACK

RK-L1-01	L1-SERVER, 42U: PP-01 U40, CM-01 U39, PP-02 U38, CM-02 U37, PP-03 U36, CM-03 U35, PP-04 U34, CM-04 U33, SW-ACC-01 U31, SW-ACC-02 U30, SW-ACC-03 U29, SW-AGG-01 U28, GW-DEMO-01 U26
RK-L1-02	L1-SERVER, 42U: SRV-DEMO-01 U20, NAS-DEMO-01 U17, PDU-01 U10, UPS-01 U1

SRV-DEMO-01 dan NAS-DEMO-01 belum punya port map; koneksinya tidak digambar.

KONSEP - BUKAN UNTUK KONSTRUKSI

STATUS KONSEP — Bukan untuk konstruksi

kantor-rpg Proyek kantor-rpg · gedung KRPG-01

Topologi jaringan (virtual)


Skala	NTS @ A3 lanskap
Revisi	P03 · 2026-10-01
Render	2026-10-02 02:42:18 UTC
Halaman	1/1
Digambar	Claude Code cloud (generator)
Diperiksa	Max (supervisor) belum review
Sumber	world.json sha256 488597bb0552fbde

Huruf: Helvetica fallback (Alegreya Sans tidak tersedia saat build).

Nomor lembar

ICT-001

Rev P03 · 1/1

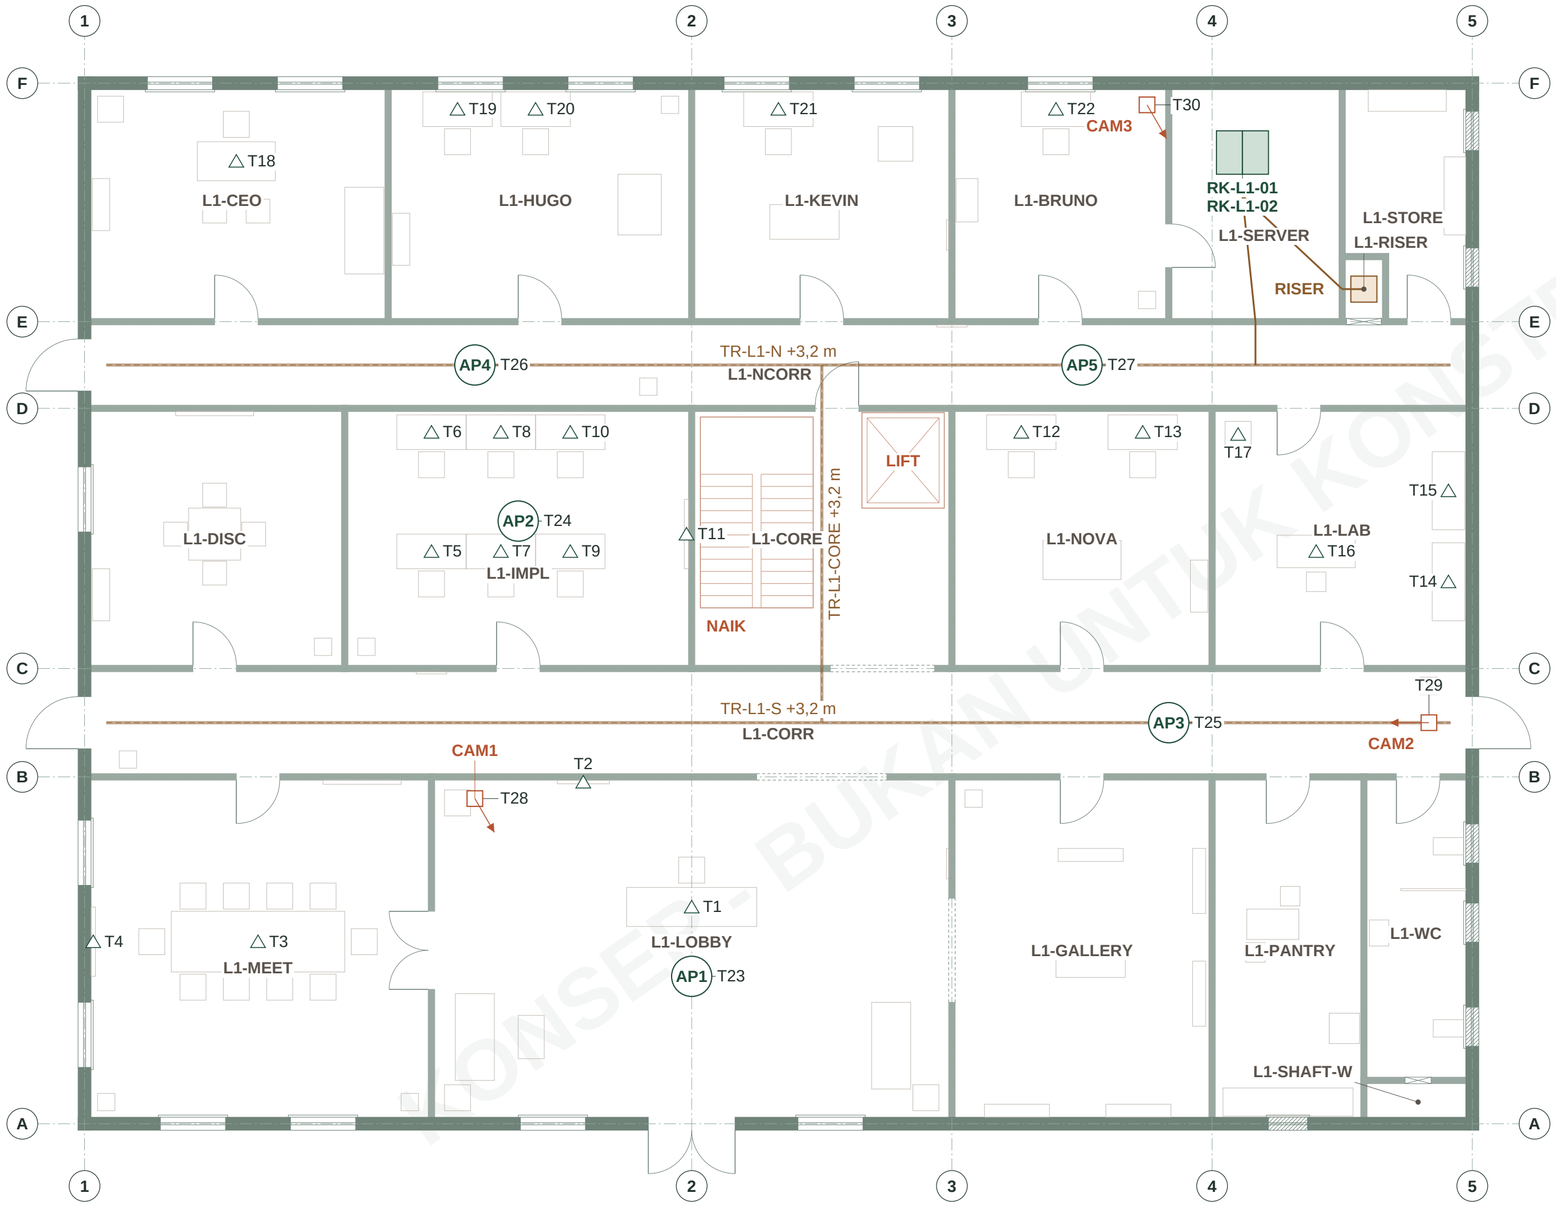

OUTLET, AP DAN KAMERA LANTAI 1 Skala 1:100 @ A2

Tag Tnn = outlet TO-L1-0nn, APn/CAMn = perangkat; ID lengkap di tabel panel. Tray di +3,2 m (AS-ICT-02). AP placeholder tanpa klaim radius Wi-Fi (AS-ICT-01).

0 1 2 5 10 m (1:100)

U

Rancangan virtual, bukan topologi produksi

Lantai L1: Lantai 1 - Kerja & Kunjungan. Sumber: world.json ict + design/derived/ict-portmap.json

LEGENDA

- △ Outlet data, tag Tnn
- ◯ AP placeholder, tag APn
- Kamera opsional + arah konsep
- Tray kabel +3,2 m
- Riser ke lantai lain
- Rack 42U (target)

OUTLET L1 (30 outlet, 55 port)

Tag	ID	Ruang	Port
T1	TO-L1-001	LOBBY	2
T2	TO-L1-002	LOBBY	1
T3	TO-L1-003	MEET	2
T4	TO-L1-004	MEET	1
T5	TO-L1-005	IMPL	2
T6	TO-L1-006	IMPL	2
T7	TO-L1-007	IMPL	2
T8	TO-L1-008	IMPL	2
T9	TO-L1-009	IMPL	2
T10	TO-L1-010	IMPL	2
T11	TO-L1-011	IMPL	1
T12	TO-L1-012	NOVA	2
T13	TO-L1-013	NOVA	2
T14	TO-L1-014	LAB	4
T15	TO-L1-015	LAB	4

Tag	ID	Ruang	Port
T16	TO-L1-016	LAB	4
T17	TO-L1-017	LAB	2
T18	TO-L1-018	CEO	2
T19	TO-L1-019	HUGO	2
T20	TO-L1-020	HUGO	2
T21	TO-L1-021	KEVIN	2
T22	TO-L1-022	BRUNO	2
T23	TO-L1-023	LOBBY	1
T24	TO-L1-024	IMPL	1
T25	TO-L1-025	CORR	1
T26	TO-L1-026	NCORR	1
T27	TO-L1-027	NCORR	1
T28	TO-L1-028	LOBBY	1
T29	TO-L1-029	CORR	1
T30	TO-L1-030	BRUNO	1

Domain dan endpoint per port: ICT-401.

PERANGKAT L1 (AP 5, kamera 3)

Tag	ID	Ruang	Outlet	z m	PoE
AP1	AP-L1-01	LOBBY	T23	3,0	4
AP2	AP-L1-02	IMPL	T24	3,0	4
AP3	AP-L1-03	CORR	T25	3,0	4
AP4	AP-L1-04	NCORR	T26	3,0	4
AP5	AP-L1-05	NCORR	T27	3,0	4
CAM1	CAM-L1-01	LOBBY	T28	2,8	3
CAM2	CAM-L1-02	CORR	T29	2,8	3
CAM3	CAM-L1-03	BRUNO	T30	2,8	3

Semua AP placeholder (AS-ICT-01); kamera opsional konsep, arah bukan FOV terukur. Lihat juga AS-ICT-02, AS-ICT-03, AS-NET-01 di A-001.

KONSEP - BUKAN UNTUK KONSTRUKSI

STATUS KONSEP Bukan untuk konstruksi

kantor-rpg Proyek kantor-rpg · gedung KRPG-01

Outlet, AP dan kamera Lantai 1


Skala	1:100 @ A2 lanskap
Revisi	P03 · 2026-10-01
Render	2026-10-02 02:42:18 UTC
Halaman	1/1
Digambar	Claude Code cloud (generator)
Diperiksa	Max (supervisor) belum review
Sumber	world.json sha256 488597bb0552fbde

Nomor lembar

ICT-101

Rev P03 · 1/1

Huruf: Helvetica fallback (Alegreya Sans tidak tersedia saat build).

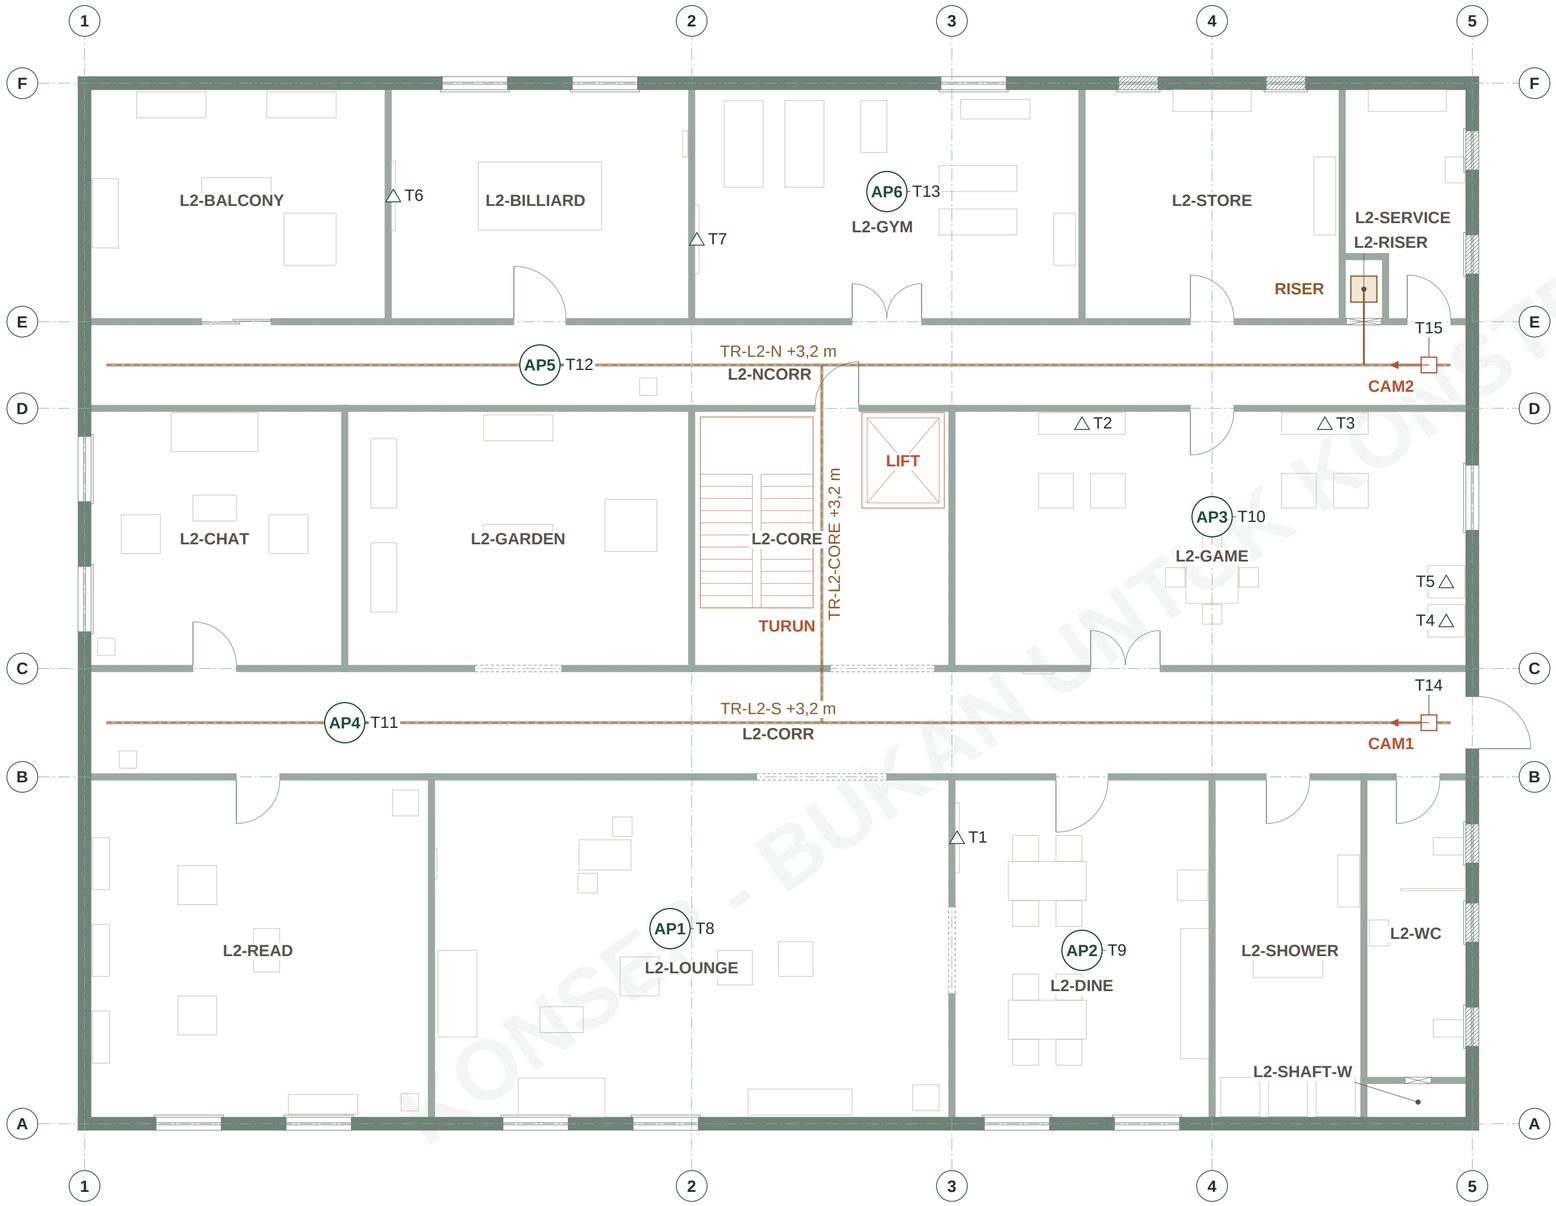

OUTLET, AP DAN KAMERA LANTAI 2 Skala 1:100 @ A2

Tag Tnn = outlet TO-L2-0nn, APn/CAMn = perangkat; ID lengkap di tabel panel. Tray di +3,2 m (AS-ICT-02). AP placeholder tanpa klaim radius Wi-Fi (AS-ICT-01).

0 1 2 5 10 m (1:100)

U

Rancangan virtual, bukan topologi produksi

Lantai L2: Lantai 2 - Rekreasi. Sumber: world.json ict + design/derived/ict-portmap.json

LEGENDA

- △ Outlet data, tag Tnn
- ○ AP placeholder, tag APn
- Kamera opsional + arah konsep
- Tray kabel +3,2 m
- Riser ke lantai lain
- Rack 42U (target)

OUTLET L2 (15 outlet, 17 port)

Tag	ID	Ruang	Port
T1	TO-L2-001	DINE	1
T2	TO-L2-002	GAME	2
T3	TO-L2-003	GAME	2
T4	TO-L2-004	GAME	1
T5	TO-L2-005	GAME	1
T6	TO-L2-006	BILLIARD	1
T7	TO-L2-007	GYM	1
T8	TO-L2-008	LOUNGE	1
T9	TO-L2-009	DINE	1
T10	TO-L2-010	GAME	1
T11	TO-L2-011	CORR	1
T12	TO-L2-012	NCORR	1
T13	TO-L2-013	GYM	1
T14	TO-L2-014	CORR	1
T15	TO-L2-015	NCORR	1

Domain dan endpoint per port: ICT-401.

PERANGKAT L2 (AP 6, kamera 2)

Tag	ID	Ruang	Outlet	z m	PoE
AP1	AP-L2-01	LOUNGE	T8	3,0	4
AP2	AP-L2-02	DINE	T9	3,0	4
AP3	AP-L2-03	GAME	T10	3,0	4
AP4	AP-L2-04	CORR	T11	3,0	4
AP5	AP-L2-05	NCORR	T12	3,0	4
AP6	AP-L2-06	GYM	T13	3,0	4
CAM1	CAM-L2-01	CORR	T14	2,8	3
CAM2	CAM-L2-02	NCORR	T15	2,8	3

Semua AP placeholder (AS-ICT-01); kamera opsional konsep, arah bukan FOV terukur. Lihat juga AS-ICT-02, AS-ICT-03, AS-NET-01 di A-001.

STATUS KONSEP Bukan untuk konstruksi

kantor-rpg Proyek kantor-rpg · gedung KRPG-01

Outlet, AP dan kamera Lantai 2

Skala	1:100 @ A2 lanskap
Revisi	P03 · 2026-10-01
Render	2026-10-02 02:42:18 UTC
Halaman	1/1
Digambar	Claude Code cloud (generator)
Diperiksa	Max (supervisor) belum review
Sumber	world.json sha256 488597bb0552fbde


Nomor lembar **ICT-102** Rev P03 · 1/1

Huruf: Helvetica fallback (Alegreya Sans tidak tersedia saat build).

KONSEP - BUKAN UNTUK KONSTRUKSI


RK-L1-01 TAMPAK DEPAN

1:10 · L1-SERVER · 42U

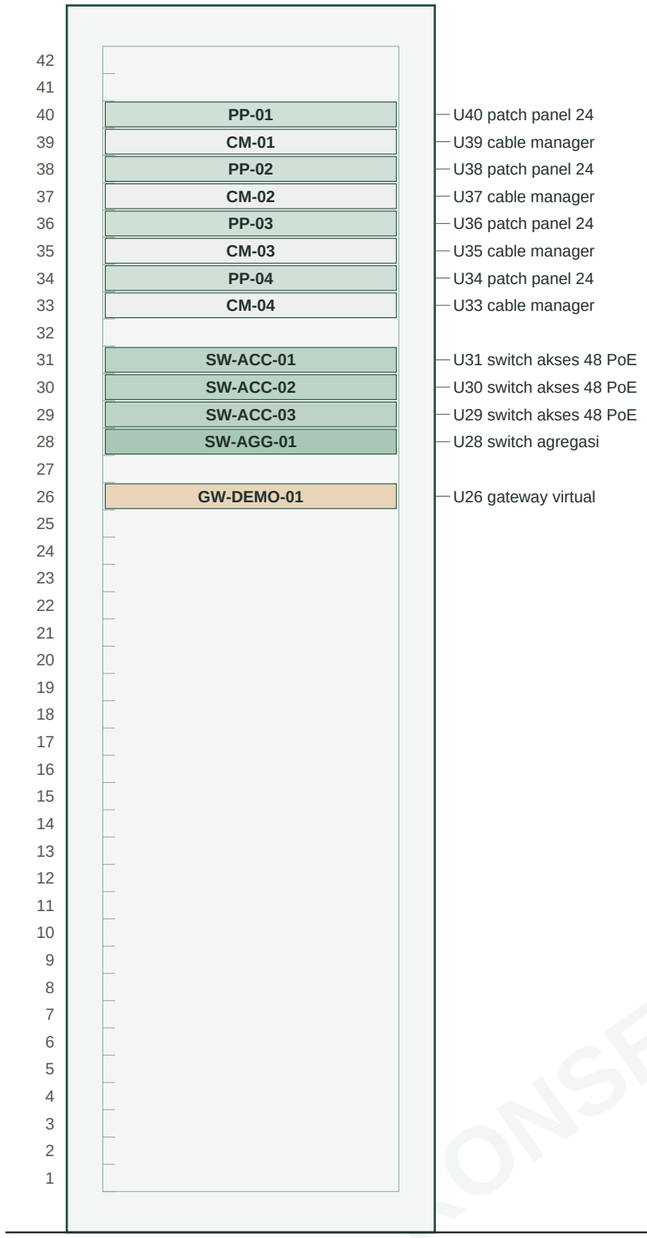


RK-L1-02 TAMPAK DEPAN

1:10 · L1-SERVER · 42U

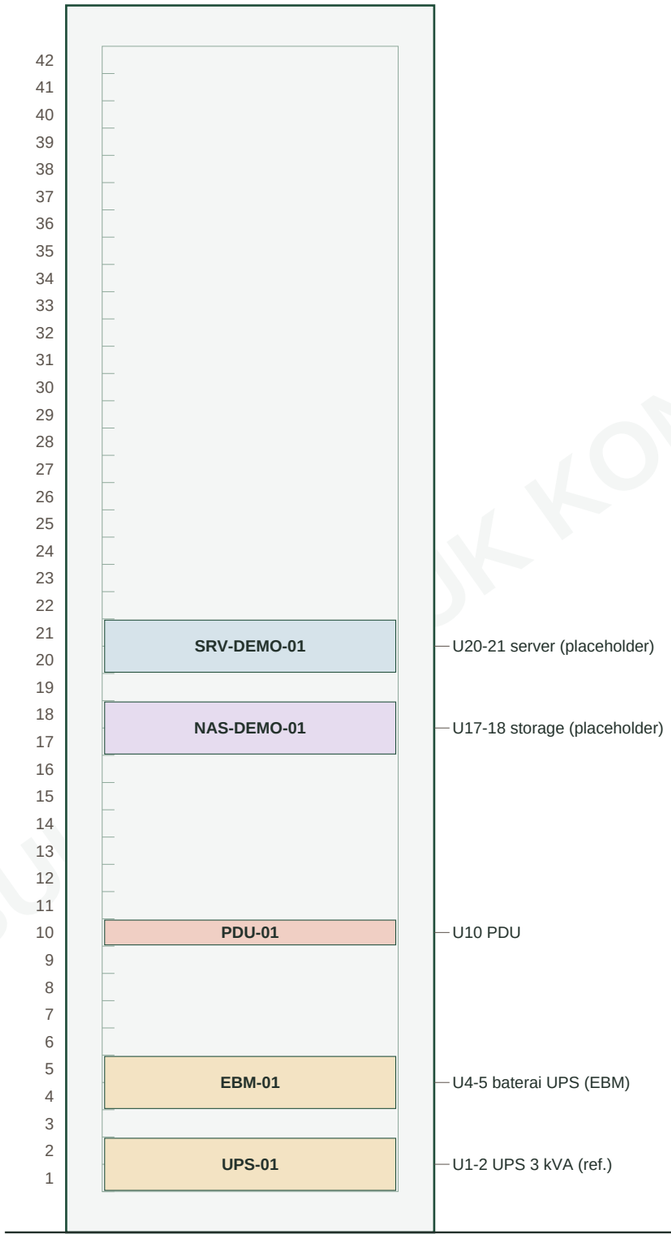

CLEARANCE RACK 1:100 (AS-ICT-06)

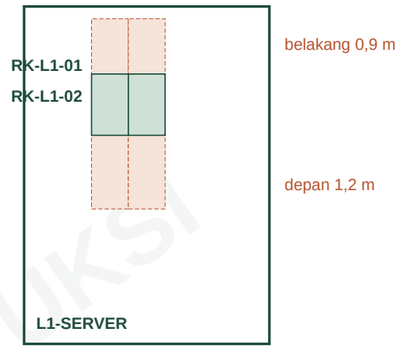

ISI RACK (world.json racks[].contents)

Rack	U	Tg	Perangkat	Tipe	Port
RK-L1-01	U40	1	PP-01	patch panel 24	24
RK-L1-01	U39	1	CM-01	cable manager	-
RK-L1-01	U38	1	PP-02	patch panel 24	24
RK-L1-01	U37	1	CM-02	cable manager	-
RK-L1-01	U36	1	PP-03	patch panel 24	24
RK-L1-01	U35	1	CM-03	cable manager	-
RK-L1-01	U34	1	PP-04	patch panel 24	24
RK-L1-01	U33	1	CM-04	cable manager	-
RK-L1-01	U31	1	SW-ACC-01	switch akses 48 PoE	48
RK-L1-01	U30	1	SW-ACC-02	switch akses 48 PoE	48
RK-L1-01	U29	1	SW-ACC-03	switch akses 48 PoE	48
RK-L1-01	U28	1	SW-AGG-01	switch agregasi	24
RK-L1-01	U26	1	GW-DEMO-01	gateway virtual	8
RK-L1-02	U20	2	SRV-DEMO-01	server (placeholder)	2
RK-L1-02	U17	2	NAS-DEMO-01	storage (placeholder)	2
RK-L1-02	U10	1	PDU-01	PDU	-
RK-L1-02	U4	2	EBM-01	baterai UPS (EBM)	-
RK-L1-02	U1	2	UPS-01	UPS 3 kVA (ref.)	-

- Skala tampak rack 1:10; 1U = 44,45 mm, nomor U dihitung dari bawah. Tg = tinggi dalam U.
- Switch, UPS 3 kVA + 1 EBM = model referensi konsep (AS-ICT-07, AS-ICT-09), bukan keputusan beli; PDU belum dipilih; tanpa harga.
- Clearance depan 1,2 m / belakang 0,9 m adalah target konsep dari catalog (AS-ICT-06), wajib diverifikasi ke standar yang dipilih.

STATUS KONSEP — Bukan untuk konstruksi

kantor-rpg Proyek kantor-rpg · gedung KRPG-01

Elevasi rack

Skala	1:10 @ A3 lanskap
Revisi	P03 · 2026-10-01
Render	2026-10-05 00:32:15 UTC
Halaman	1/1
Digambar	Claude Code cloud (generator)
Diperiksa	Max (supervisor) belum review
Sumber	world.json sha256 5094f43e94ea4719

Huruf: Helvetica fallback (Alegreya Sans tidak tersedia saat build).

Nomor lembar


ICT-201

Rev P03 · 1/1

KONSEP - BUKAN UNTUK KONSTRUKSI


JALUR KABEL L1

1:200 · tray +3,2 m

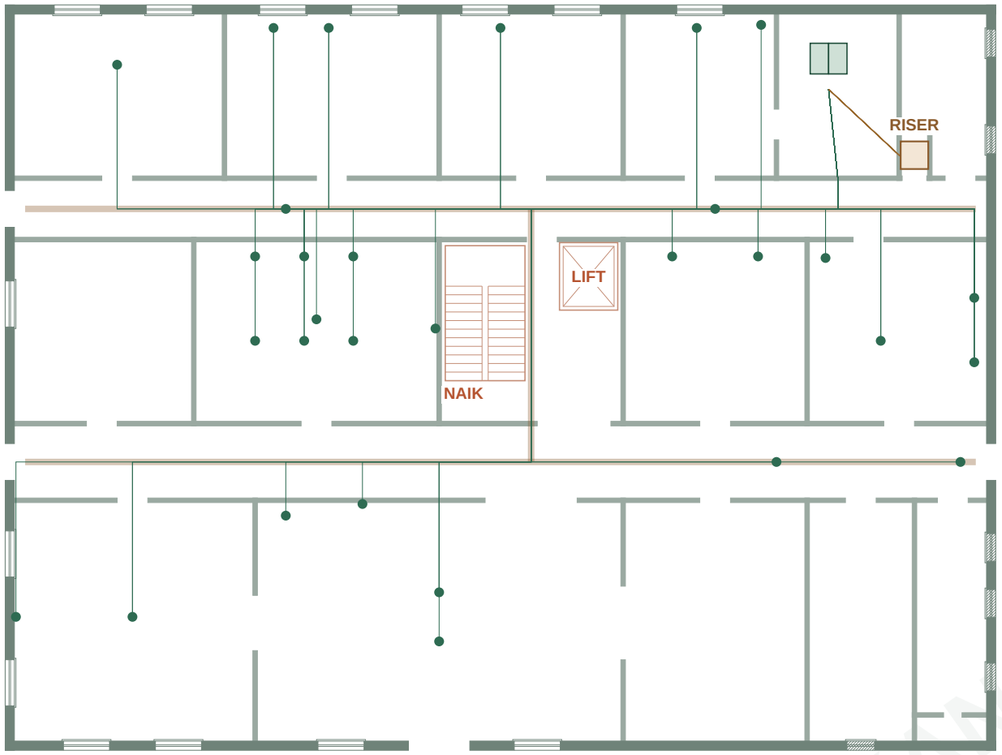

JALUR KABEL L2

1:200 · tray +3,2 m

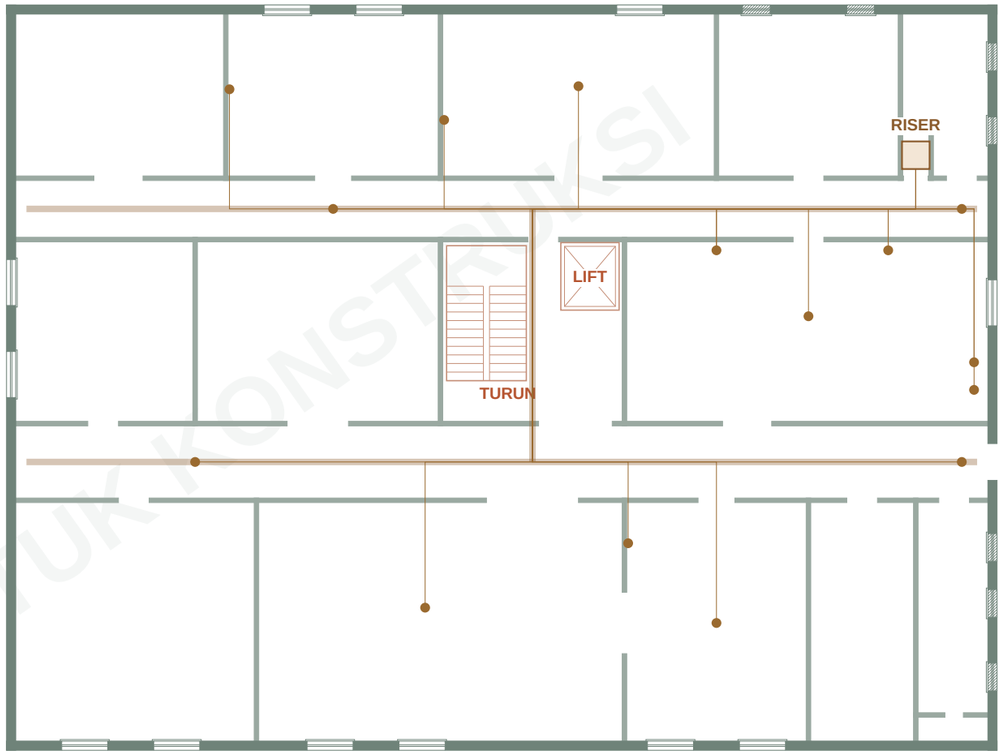


RINGKASAN PANJANG KABEL (ict-portmap.json)

Lantai	Kabel	Total m	Min m	Maks m	Rata m
L1	55	1537,1	12,7	50,6	27,9
L2	17	537,7	15,6	48,9	31,6
Total	72	2074,8	12,7	50,6	28,8

Cek: jumlah baris 2074,8 m vs total port map 2074,8 m: COCOK. Semua kabel di bawah target 90 m (AS-ICT-03).

SKEMA RISER

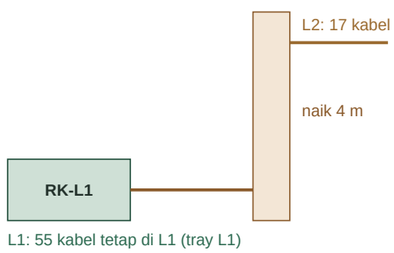

- Garis hijau = kabel endpoint L1, coklat = kabel endpoint L2 (bagian di L1 ikut warna lantai tujuan).
- Panjang = route tray + naik rack 1,2 m + riser 4,0 m (L2) + drop + slack 3,3 m (AS-ICT-02).

0 2 5 10 20 m (1:200)

STATUS KONSEP — Bukan untuk konstruksi

kantor-rpg Proyek kantor-rpg · gedung KRPG-01

Pathway dan riser

Skala	1:200 @ A3 lanskap
Revisi	P03 · 2026-10-01
Render	2026-10-02 02:42:18 UTC
Halaman	1/1
Digambar	Claude Code cloud (generator)
Diperiksa	Max (supervisor) belum review
Sumber	world.json sha256 488597bb0552fbde

Huruf: Helvetica fallback (Alegreya Sans tidak tersedia saat build).

Nomor lembar

ICT-301

Rev P03 · 1/1

KONSEP - BUKAN UNTUK KONSTRUKSI

PORT SCHEDULE

rancangan virtual, bukan topologi produksi · sumber design/derived/ict-portmap.json (world P03)

Kabel	Port outlet	Ruang	PP/port	Switch/port	Domain	PoE	m	Label sisi rack	Label sisi outlet	Endpoint
C-TO-L1-023-A	TO-L1-023-A	L1-LOBBY	PP-01/01	SW-ACC-01/01	NET-OFFICE	4	35,8	PP-01-01 > TO-L1-023-A	TO-L1-023-A > PP-01-01	ap AP-L1-01
C-TO-L1-024-A	TO-L1-024-A	L1-IMPL	PP-01/02	SW-ACC-01/02	NET-OFFICE	4	29,3	PP-01-02 > TO-L1-024-A	TO-L1-024-A > PP-01-02	ap AP-L1-02
C-TO-L1-025-A	TO-L1-025-A	L1-CORR	PP-01/03	SW-ACC-01/03	NET-OFFICE	4	34,9	PP-01-03 > TO-L1-025-A	TO-L1-025-A > PP-01-03	ap AP-L1-03
C-TO-L1-026-A	TO-L1-026-A	L1-NCORR	PP-01/04	SW-ACC-01/04	NET-OFFICE	4	26,7	PP-01-04 > TO-L1-026-A	TO-L1-026-A > PP-01-04	ap AP-L1-04
C-TO-L1-027-A	TO-L1-027-A	L1-NCORR	PP-01/05	SW-ACC-01/05	NET-OFFICE	4	12,7	PP-01-05 > TO-L1-027-A	TO-L1-027-A > PP-01-05	ap AP-L1-05
C-TO-L1-028-A	TO-L1-028-A	L1-LOBBY	PP-01/06	SW-ACC-01/06	NET-OFFICE	3	36,7	PP-01-06 > TO-L1-028-A	TO-L1-028-A > PP-01-06	camera CAM-L1-01
C-TO-L1-029-A	TO-L1-029-A	L1-CORR	PP-01/07	SW-ACC-01/07	NET-OFFICE	3	40,9	PP-01-07 > TO-L1-029-A	TO-L1-029-A > PP-01-07	camera CAM-L1-02
C-TO-L1-030-A	TO-L1-030-A	L1-BRUNO	PP-01/08	SW-ACC-01/08	NET-OFFICE	3	17,2	PP-01-08 > TO-L1-030-A	TO-L1-030-A > PP-01-08	camera CAM-L1-03
C-TO-L2-008-A	TO-L2-008-A	L2-LOUNGE	PP-01/09	SW-ACC-01/09	NET-OFFICE	4	43,1	PP-01-09 > TO-L2-008-A	TO-L2-008-A > PP-01-09	ap AP-L2-01
C-TO-L2-009-A	TO-L2-009-A	L2-DINE	PP-01/10	SW-ACC-01/10	NET-OFFICE	4	46,1	PP-01-10 > TO-L2-009-A	TO-L2-009-A > PP-01-10	ap AP-L2-02
C-TO-L2-010-A	TO-L2-010-A	L2-GAME	PP-01/11	SW-ACC-01/11	NET-OFFICE	4	21,1	PP-01-11 > TO-L2-010-A	TO-L2-010-A > PP-01-11	ap AP-L2-03
C-TO-L2-011-A	TO-L2-011-A	L2-CORR	PP-01/12	SW-ACC-01/12	NET-OFFICE	4	45,9	PP-01-12 > TO-L2-011-A	TO-L2-011-A > PP-01-12	ap AP-L2-04
C-TO-L2-012-A	TO-L2-012-A	L2-NCORR	PP-01/13	SW-ACC-01/13	NET-OFFICE	4	33,1	PP-01-13 > TO-L2-012-A	TO-L2-012-A > PP-01-13	ap AP-L2-05
C-TO-L2-013-A	TO-L2-013-A	L2-GYM	PP-01/14	SW-ACC-01/14	NET-OFFICE	4	29,1	PP-01-14 > TO-L2-013-A	TO-L2-013-A > PP-01-14	ap AP-L2-06
C-TO-L2-014-A	TO-L2-014-A	L2-CORR	PP-01/15	SW-ACC-01/15	NET-OFFICE	3	48,9	PP-01-15 > TO-L2-014-A	TO-L2-014-A > PP-01-15	camera CAM-L2-01
C-TO-L2-015-A	TO-L2-015-A	L2-NCORR	PP-01/16	SW-ACC-01/16	NET-OFFICE	3	15,6	PP-01-16 > TO-L2-015-A	TO-L2-015-A > PP-01-16	camera CAM-L2-02
C-TO-L1-001-A	TO-L1-001-A	L1-LOBBY	PP-01/17	SW-ACC-01/17	NET-OFFICE	-	36,9	PP-01-17 > TO-L1-001-A	TO-L1-001-A > PP-01-17	workstation FX-L1-001
C-TO-L1-001-B	TO-L1-001-B	L1-LOBBY	PP-01/18	SW-ACC-01/18	NET-OFFICE	-	36,9	PP-01-18 > TO-L1-001-B	TO-L1-001-B > PP-01-18	printer FX-L1-001
C-TO-L1-002-A	TO-L1-002-A	L1-LOBBY	PP-01/19	SW-ACC-01/19	NET-DEMO	-	35,6	PP-01-19 > TO-L1-002-A	TO-L1-002-A > PP-01-19	signage FX-L1-009
C-TO-L1-003-A	TO-L1-003-A	L1-MEET	PP-01/20	SW-ACC-01/20	NET-OFFICE	-	47,7	PP-01-20 > TO-L1-003-A	TO-L1-003-A > PP-01-20	table_box FX-L1-011
C-TO-L1-003-B	TO-L1-003-B	L1-MEET	PP-01/21	SW-ACC-01/21	NET-OFFICE	-	47,7	PP-01-21 > TO-L1-003-B	TO-L1-003-B > PP-01-21	spare FX-L1-011
C-TO-L1-004-A	TO-L1-004-A	L1-MEET	PP-01/22	SW-ACC-01/22	NET-OFFICE	-	50,6	PP-01-22 > TO-L1-004-A	TO-L1-004-A > PP-01-22	display FX-L1-022
C-TO-L1-005-A	TO-L1-005-A	L1-IMPL	PP-01/23	SW-ACC-01/23	NET-OFFICE	-	34,7	PP-01-23 > TO-L1-005-A	TO-L1-005-A > PP-01-23	workstation FX-L1-053
C-TO-L1-005-B	TO-L1-005-B	L1-IMPL	PP-01/24	SW-ACC-01/24	NET-OFFICE	-	34,7	PP-01-24 > TO-L1-005-B	TO-L1-005-B > PP-01-24	phone_or_spare FX-L1-053
C-TO-L1-006-A	TO-L1-006-A	L1-IMPL	PP-02/01	SW-ACC-02/01	NET-OFFICE	-	31,9	PP-02-01 > TO-L1-006-A	TO-L1-006-A > PP-02-01	workstation FX-L1-055
C-TO-L1-006-B	TO-L1-006-B	L1-IMPL	PP-02/02	SW-ACC-02/02	NET-OFFICE	-	31,9	PP-02-02 > TO-L1-006-B	TO-L1-006-B > PP-02-02	phone_or_spare FX-L1-055
C-TO-L1-007-A	TO-L1-007-A	L1-IMPL	PP-02/03	SW-ACC-02/03	NET-OFFICE	-	33,1	PP-02-03 > TO-L1-007-A	TO-L1-007-A > PP-02-03	workstation FX-L1-057
C-TO-L1-007-B	TO-L1-007-B	L1-IMPL	PP-02/04	SW-ACC-02/04	NET-OFFICE	-	33,1	PP-02-04 > TO-L1-007-B	TO-L1-007-B > PP-02-04	phone_or_spare FX-L1-057
C-TO-L1-008-A	TO-L1-008-A	L1-IMPL	PP-02/05	SW-ACC-02/05	NET-OFFICE	-	30,3	PP-02-05 > TO-L1-008-A	TO-L1-008-A > PP-02-05	workstation FX-L1-059
C-TO-L1-008-B	TO-L1-008-B	L1-IMPL	PP-02/06	SW-ACC-02/06	NET-OFFICE	-	30,3	PP-02-06 > TO-L1-008-B	TO-L1-008-B > PP-02-06	phone_or_spare FX-L1-059
C-TO-L1-009-A	TO-L1-009-A	L1-IMPL	PP-02/07	SW-ACC-02/07	NET-OFFICE	-	31,5	PP-02-07 > TO-L1-009-A	TO-L1-009-A > PP-02-07	workstation FX-L1-061
C-TO-L1-009-B	TO-L1-009-B	L1-IMPL	PP-02/08	SW-ACC-02/08	NET-OFFICE	-	31,5	PP-02-08 > TO-L1-009-B	TO-L1-009-B > PP-02-08	phone_or_spare FX-L1-061
C-TO-L1-010-A	TO-L1-010-A	L1-IMPL	PP-02/09	SW-ACC-02/09	NET-OFFICE	-	28,7	PP-02-09 > TO-L1-010-A	TO-L1-010-A > PP-02-09	workstation FX-L1-063
C-TO-L1-010-B	TO-L1-010-B	L1-IMPL	PP-02/10	SW-ACC-02/10	NET-OFFICE	-	28,7	PP-02-10 > TO-L1-010-B	TO-L1-010-B > PP-02-10	phone_or_spare FX-L1-063
C-TO-L1-011-A	TO-L1-011-A	L1-IMPL	PP-02/11	SW-ACC-02/11	NET-OFFICE	-	27,5	PP-02-11 > TO-L1-011-A	TO-L1-011-A > PP-02-11	display FX-L1-065
C-TO-L1-012-A	TO-L1-012-A	L1-NOVA	PP-02/12	SW-ACC-02/12	NET-OFFICE	-	18,3	PP-02-12 > TO-L1-012-A	TO-L1-012-A > PP-02-12	workstation FX-L1-069
C-TO-L1-012-B	TO-L1-012-B	L1-NOVA	PP-02/13	SW-ACC-02/13	NET-OFFICE	-	18,3	PP-02-13 > TO-L1-012-B	TO-L1-012-B > PP-02-13	phone_or_spare FX-L1-069
C-TO-L1-013-A	TO-L1-013-A	L1-NOVA	PP-02/14	SW-ACC-02/14	NET-OFFICE	-	15,5	PP-02-14 > TO-L1-013-A	TO-L1-013-A > PP-02-14	workstation FX-L1-071
C-TO-L1-013-B	TO-L1-013-B	L1-NOVA	PP-02/15	SW-ACC-02/15	NET-OFFICE	-	15,5	PP-02-15 > TO-L1-013-B	TO-L1-013-B > PP-02-15	phone_or_spare FX-L1-071
C-TO-L1-014-A	TO-L1-014-A	L1-LAB	PP-02/16	SW-ACC-02/16	NET-LAB	-	20,8	PP-02-16 > TO-L1-014-A	TO-L1-014-A > PP-02-16	lab_device FX-L1-075
C-TO-L1-014-B	TO-L1-014-B	L1-LAB	PP-02/17	SW-ACC-02/17	NET-LAB	-	20,8	PP-02-17 > TO-L1-014-B	TO-L1-014-B > PP-02-17	lab_device FX-L1-075
C-TO-L1-014-C	TO-L1-014-C	L1-LAB	PP-02/18	SW-ACC-02/18	NET-LAB	-	20,8	PP-02-18 > TO-L1-014-C	TO-L1-014-C > PP-02-18	lab_device FX-L1-075
C-TO-L1-014-D	TO-L1-014-D	L1-LAB	PP-02/19	SW-ACC-02/19	NET-LAB	-	20,8	PP-02-19 > TO-L1-014-D	TO-L1-014-D > PP-02-19	lab_device FX-L1-075
C-TO-L1-015-A	TO-L1-015-A	L1-LAB	PP-02/20	SW-ACC-02/20	NET-LAB	-	18,7	PP-02-20 > TO-L1-015-A	TO-L1-015-A > PP-02-20	lab_device FX-L1-076

Label dua ujung: sisi rack 'PP-nn-pp > port outlet', sisi outlet sebaliknya. Panjang mengikuti AS-ICT-02; batas 90 m AS-ICT-03.

STATUS KONSEP — Bukan untuk konstruksi

kantor-rpg Proyek kantor-rpg · gedung KRPG-01

Port dan device schedule

Skala NTS @ A3 lanskap
Revisi P03 · 2026-10-01
Render 2026-10-02 02:42:18 UTC
Halaman 1/3
Digambar Claude Code cloud (generator)
Diperiksa Max (supervisor) belum review
Sumber world.json sha256 488597bb0552fbde

Huruf: Helvetica fallback (Alegreya Sans tidak tersedia saat build).

Nomor lembar

ICT-401

Rev P03 · 1/3

PORT SCHEDULE

rancangan virtual, bukan topologi produksi · sumber design/derived/ict-portmap.json (world P03)

Kabel	Port outlet	Ruang	PP/port	Switch/port	Domain	PoE	m	Label sisi rack	Label sisi outlet	Endpoint
C-TO-L1-015-B	TO-L1-015-B	L1-LAB	PP-02/21	SW-ACC-02/21	NET-LAB	-	18,7	PP-02-21 > TO-L1-015-B	TO-L1-015-B > PP-02-21	lab_device FX-L1-076
C-TO-L1-015-C	TO-L1-015-C	L1-LAB	PP-02/22	SW-ACC-02/22	NET-LAB	-	18,7	PP-02-22 > TO-L1-015-C	TO-L1-015-C > PP-02-22	lab_device FX-L1-076
C-TO-L1-015-D	TO-L1-015-D	L1-LAB	PP-02/23	SW-ACC-02/23	NET-LAB	-	18,7	PP-02-23 > TO-L1-015-D	TO-L1-015-D > PP-02-23	lab_device FX-L1-076
C-TO-L1-016-A	TO-L1-016-A	L1-LAB	PP-02/24	SW-ACC-02/24	NET-LAB	-	17,1	PP-02-24 > TO-L1-016-A	TO-L1-016-A > PP-02-24	lab_device FX-L1-077
C-TO-L1-016-B	TO-L1-016-B	L1-LAB	PP-03/01	SW-ACC-03/01	NET-LAB	-	17,1	PP-03-01 > TO-L1-016-B	TO-L1-016-B > PP-03-01	lab_device FX-L1-077
C-TO-L1-016-C	TO-L1-016-C	L1-LAB	PP-03/02	SW-ACC-03/02	NET-LAB	-	17,1	PP-03-02 > TO-L1-016-C	TO-L1-016-C > PP-03-02	lab_device FX-L1-077
C-TO-L1-016-D	TO-L1-016-D	L1-LAB	PP-03/03	SW-ACC-03/03	NET-LAB	-	17,1	PP-03-03 > TO-L1-016-D	TO-L1-016-D > PP-03-03	lab_device FX-L1-077
C-TO-L1-017-A	TO-L1-017-A	L1-LAB	PP-03/04	SW-ACC-03/04	NET-LAB	-	13,4	PP-03-04 > TO-L1-017-A	TO-L1-017-A > PP-03-04	lab_uplink FX-L1-079
C-TO-L1-017-B	TO-L1-017-B	L1-LAB	PP-03/05	SW-ACC-03/05	NET-LAB	-	13,4	PP-03-05 > TO-L1-017-B	TO-L1-017-B > PP-03-05	spare FX-L1-079
C-TO-L1-018-A	TO-L1-018-A	L1-CEO	PP-03/06	SW-ACC-03/06	NET-OFFICE	-	39,6	PP-03-06 > TO-L1-018-A	TO-L1-018-A > PP-03-06	workstation FX-L1-082
C-TO-L1-018-B	TO-L1-018-B	L1-CEO	PP-03/07	SW-ACC-03/07	NET-OFFICE	-	39,6	PP-03-07 > TO-L1-018-B	TO-L1-018-B > PP-03-07	phone_or_spare FX-L1-082
C-TO-L1-019-A	TO-L1-019-A	L1-HUGO	PP-03/08	SW-ACC-03/08	NET-OFFICE	-	35,7	PP-03-08 > TO-L1-019-A	TO-L1-019-A > PP-03-08	workstation FX-L1-089
C-TO-L1-019-B	TO-L1-019-B	L1-HUGO	PP-03/09	SW-ACC-03/09	NET-OFFICE	-	35,7	PP-03-09 > TO-L1-019-B	TO-L1-019-B > PP-03-09	phone_or_spare FX-L1-089
C-TO-L1-020-A	TO-L1-020-A	L1-HUGO	PP-03/10	SW-ACC-03/10	NET-OFFICE	-	33,9	PP-03-10 > TO-L1-020-A	TO-L1-020-A > PP-03-10	workstation FX-L1-091
C-TO-L1-020-B	TO-L1-020-B	L1-HUGO	PP-03/11	SW-ACC-03/11	NET-OFFICE	-	33,9	PP-03-11 > TO-L1-020-B	TO-L1-020-B > PP-03-11	phone_or_spare FX-L1-091
C-TO-L1-021-A	TO-L1-021-A	L1-KEVIN	PP-03/12	SW-ACC-03/12	NET-OFFICE	-	28,3	PP-03-12 > TO-L1-021-A	TO-L1-021-A > PP-03-12	workstation FX-L1-096
C-TO-L1-021-B	TO-L1-021-B	L1-KEVIN	PP-03/13	SW-ACC-03/13	NET-OFFICE	-	28,3	PP-03-13 > TO-L1-021-B	TO-L1-021-B > PP-03-13	phone_or_spare FX-L1-096
C-TO-L1-022-A	TO-L1-022-A	L1-BRUNO	PP-03/14	SW-ACC-03/14	NET-OFFICE	-	21,9	PP-03-14 > TO-L1-022-A	TO-L1-022-A > PP-03-14	workstation FX-L1-101
C-TO-L1-022-B	TO-L1-022-B	L1-BRUNO	PP-03/15	SW-ACC-03/15	NET-OFFICE	-	21,9	PP-03-15 > TO-L1-022-B	TO-L1-022-B > PP-03-15	phone_or_spare FX-L1-101
C-TO-L2-001-A	TO-L2-001-A	L2-DINE	PP-03/16	SW-ACC-03/16	NET-DEMO	-	42,5	PP-03-16 > TO-L2-001-A	TO-L2-001-A > PP-03-16	display FX-L2-034
C-TO-L2-002-A	TO-L2-002-A	L2-GAME	PP-03/17	SW-ACC-03/17	NET-DEMO	-	24,7	PP-03-17 > TO-L2-002-A	TO-L2-002-A > PP-03-17	console FX-L2-058
C-TO-L2-002-B	TO-L2-002-B	L2-GAME	PP-03/18	SW-ACC-03/18	NET-DEMO	-	24,7	PP-03-18 > TO-L2-002-B	TO-L2-002-B > PP-03-18	display FX-L2-058
C-TO-L2-003-A	TO-L2-003-A	L2-GAME	PP-03/19	SW-ACC-03/19	NET-DEMO	-	19,1	PP-03-19 > TO-L2-003-A	TO-L2-003-A > PP-03-19	console FX-L2-061
C-TO-L2-003-B	TO-L2-003-B	L2-GAME	PP-03/20	SW-ACC-03/20	NET-DEMO	-	19,1	PP-03-20 > TO-L2-003-B	TO-L2-003-B > PP-03-20	display FX-L2-061
C-TO-L2-004-A	TO-L2-004-A	L2-GAME	PP-03/21	SW-ACC-03/21	NET-DEMO	-	24,6	PP-03-21 > TO-L2-004-A	TO-L2-004-A > PP-03-21	arcade FX-L2-064
C-TO-L2-005-A	TO-L2-005-A	L2-GAME	PP-03/22	SW-ACC-03/22	NET-DEMO	-	23,7	PP-03-22 > TO-L2-005-A	TO-L2-005-A > PP-03-22	arcade FX-L2-065
C-TO-L2-006-A	TO-L2-006-A	L2-BILLIARD	PP-03/23	SW-ACC-03/23	NET-DEMO	-	42,2	PP-03-23 > TO-L2-006-A	TO-L2-006-A > PP-03-23	display FX-L2-079
C-TO-L2-007-A	TO-L2-007-A	L2-GYM	PP-03/24	SW-ACC-03/24	NET-DEMO	-	34,2	PP-03-24 > TO-L2-007-A	TO-L2-007-A > PP-03-24	display FX-L2-087
Total	72 kabel						2074,8	port map: 2074,8 m	COCOK	

Label dua ujung: sisi rack 'PP-nn-pp > port outlet', sisi outlet sebaliknya. Panjang mengikuti AS-ICT-02; batas 90 m AS-ICT-03.

KONSEP - BUKAN

STATUS KONSEP — Bukan untuk konstruksi

kantor-rpg Proyek kantor-rpg · gedung KRPG-01

Port dan device schedule

Skala	NTS @ A3 lanskap
Revisi	P03 · 2026-10-01
Render	2026-10-02 02:42:18 UTC
Halaman	2/3
Digambar	Claude Code cloud (generator)
Diperiksa	Max (supervisor) belum review
Sumber	world.json sha256 488597bb0552fbde

Huruf: Helvetica fallback (Alegreya Sans tidak tersedia saat build).

Nomor lembar

ICT-401

Rev P03 · 2/3

BOM RINGKAS DAN POE

BOM (tanpa harga): jumlah turunan dari port map; tanpa harga (AS-ICT-05)

Item	Satuan	Jumlah
Kabel tembaga horizontal (kategori TBD)	m	2074,8
Box kabel 305 m (pembulatan, belum termasuk waste)	box	7
Keystone jack sisi outlet	pcs	72
Faceplate 1 port	pcs	24
Faceplate 2 port	pcs	18
Faceplate 4 port	pcs	3
Patch panel 24 port	pcs	4
Patch cord sisi rack (1 per port terpakai, asumsi)	pcs	72
Patch cord sisi perangkat (1 per port terpakai, asumsi)	pcs	72
Access switch 48 port PoE (kelas, model TBD)	pcs	3
Access point (placeholder AS-ICT-01)	pcs	11
Kamera konsep (opsional)	pcs	5
Rack 42U (target)	pcs	2
UPS (rating TBD)	pcs	1

Harga: tidak ada (tidak ada quote bertanggal; tidak diestimasi; AS-ICT-05).

POE PER SWITCH (BELUM DIVALIDASI)

Switch	Port	Spare	Worst W	Budget W	Status
SW-ACC-01	24/48	20	407	belum ada	belum divalidasi: datasheet switch belum dipilih
SW-ACC-02	24/48	20	0	belum ada	belum divalidasi: datasheet switch belum dipilih
SW-ACC-03	24/48	20	0	belum ada	belum divalidasi: datasheet switch belum dipilih

Total PoE worst-case 407 W dari nilai PSE kelas IEEE (AS-ICT-04): belum divalidasi karena datasheet switch belum dipilih.

TOTAL

Outlet / port	45 / 72
Panjang kabel	2074,8 m (baris) vs 2074,8 m (port map): COCOK
Terpanjang / terpendek	50,6 / 12,7 m
Revisi data	port map P03 / world P03: sama

KONSEP - BUKAN UNTUK KONSTRUKSI

STATUS KONSEP — Bukan untuk konstruksi

kantor-rpg Proyek kantor-rpg · gedung KRPG-01

Port dan device schedule

Skala	NTS @ A3 lanskap
Revisi	P03 · 2026-10-01
Render	2026-10-02 02:42:18 UTC
Halaman	3/3
Digambar	Claude Code cloud (generator)
Diperiksa	Max (supervisor) belum review
Sumber	world.json sha256 488597bb0552fbde

Huruf: Helvetica fallback (Alegreya Sans tidak tersedia saat build).

Nomor lembar

ICT-401

Rev P03 · 3/3